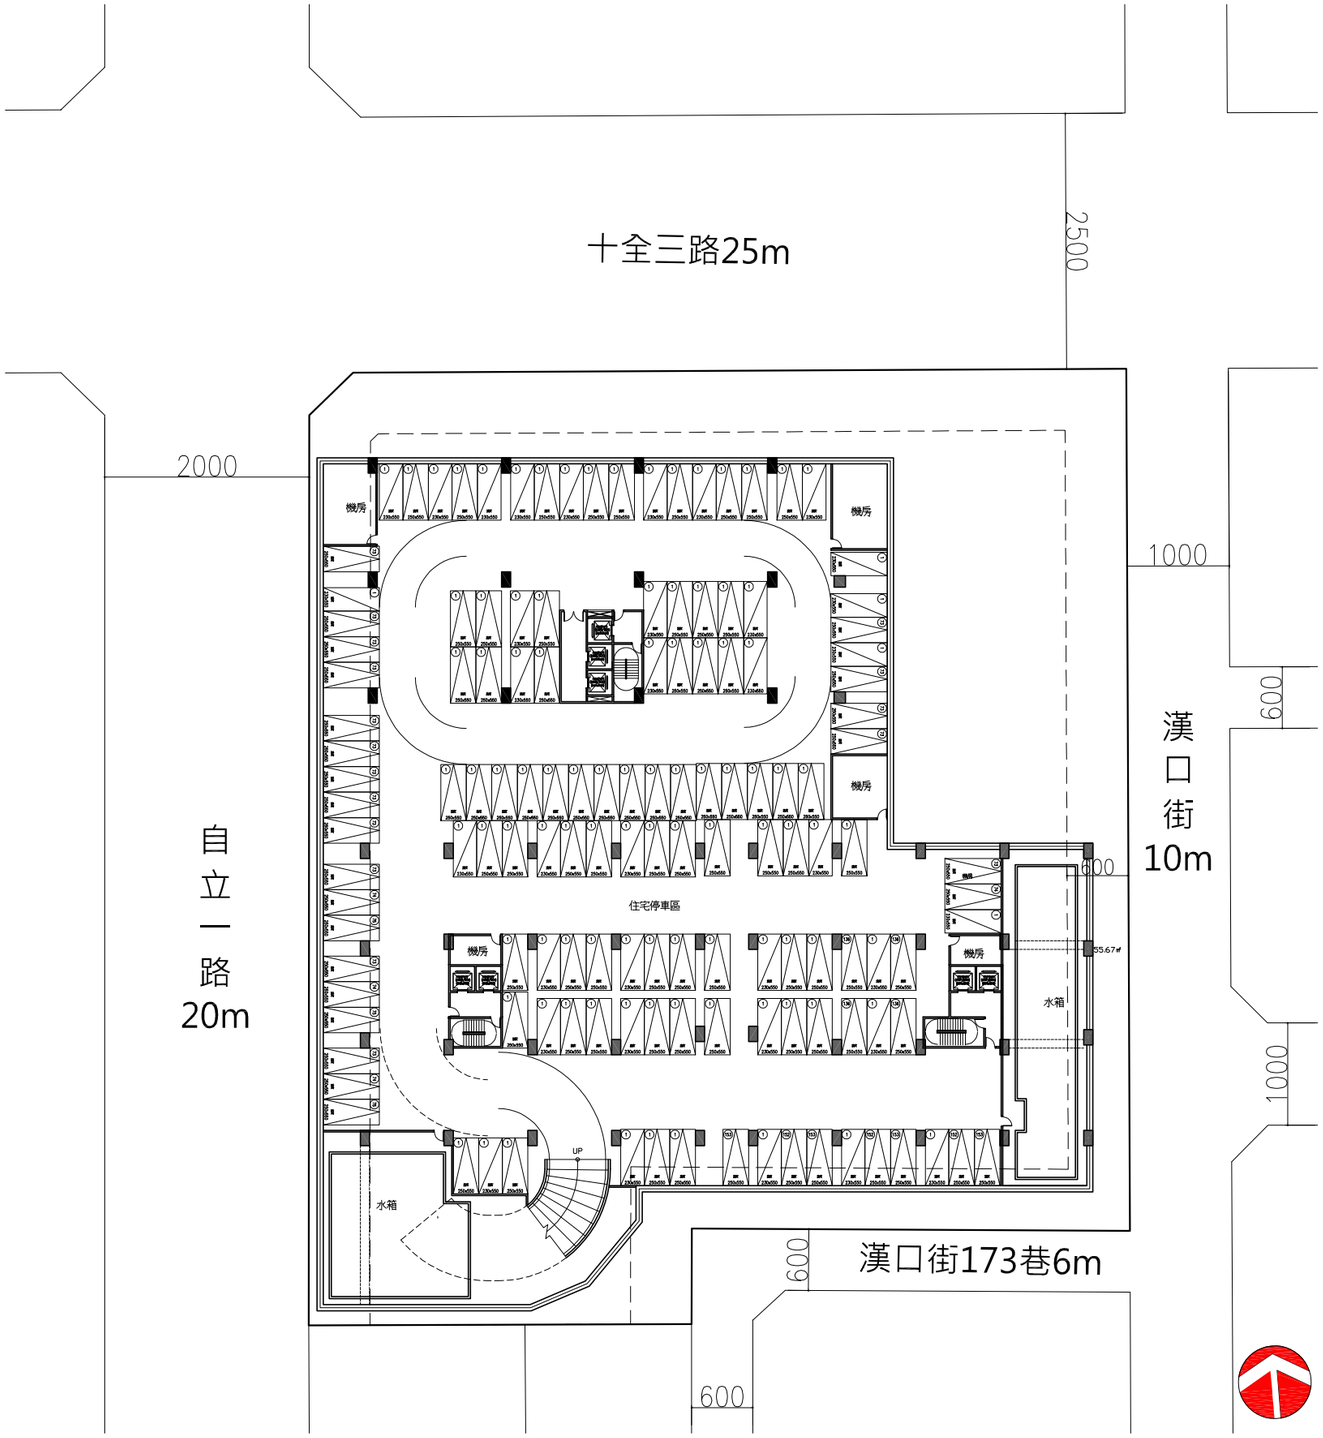

住宅汽車137台

高雄市三民區住宅案 Scheme 01

地下五層平面圖S:1/600

李祖原聯合建築師事務所
C.Y.LEE & PARTNERS Architects / Planners

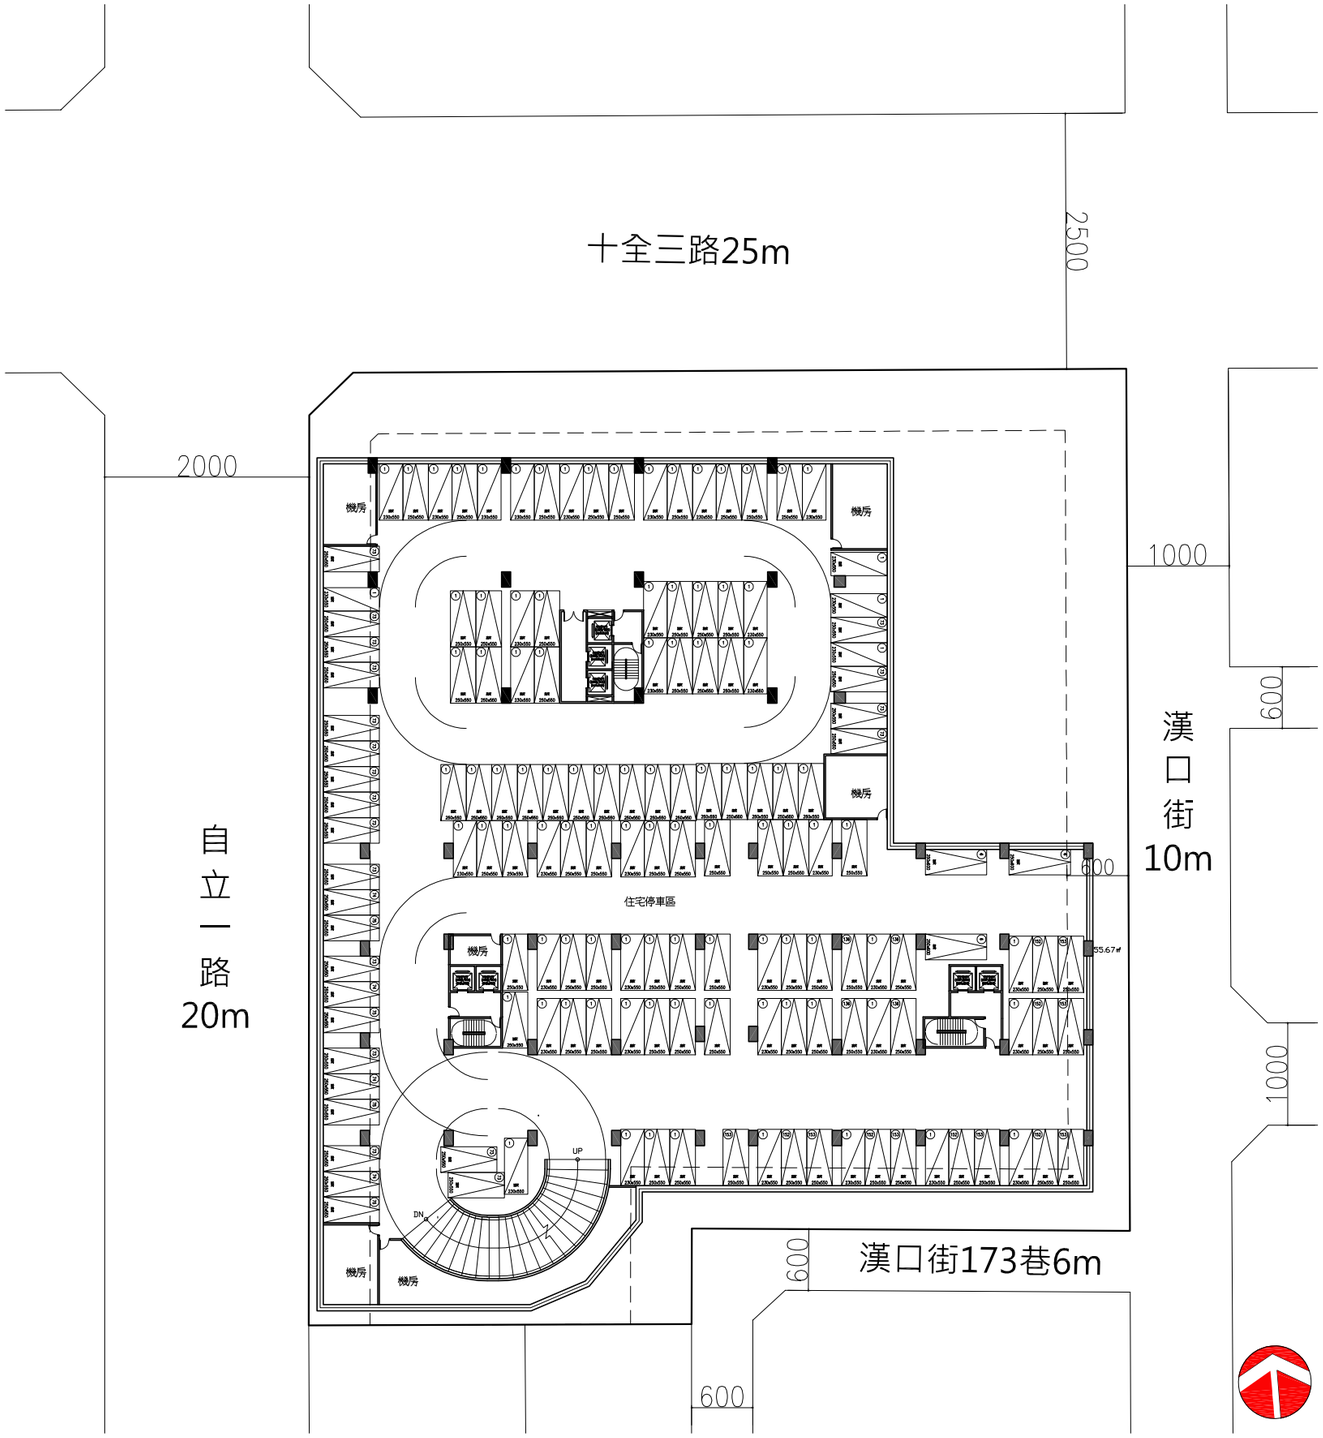

高雄市三民區住宅案 Scheme 01

地下四層平面圖S:1/600

李祖原聯合建築師事務所
C.Y.LEE & PARTNERS Architects / Planners

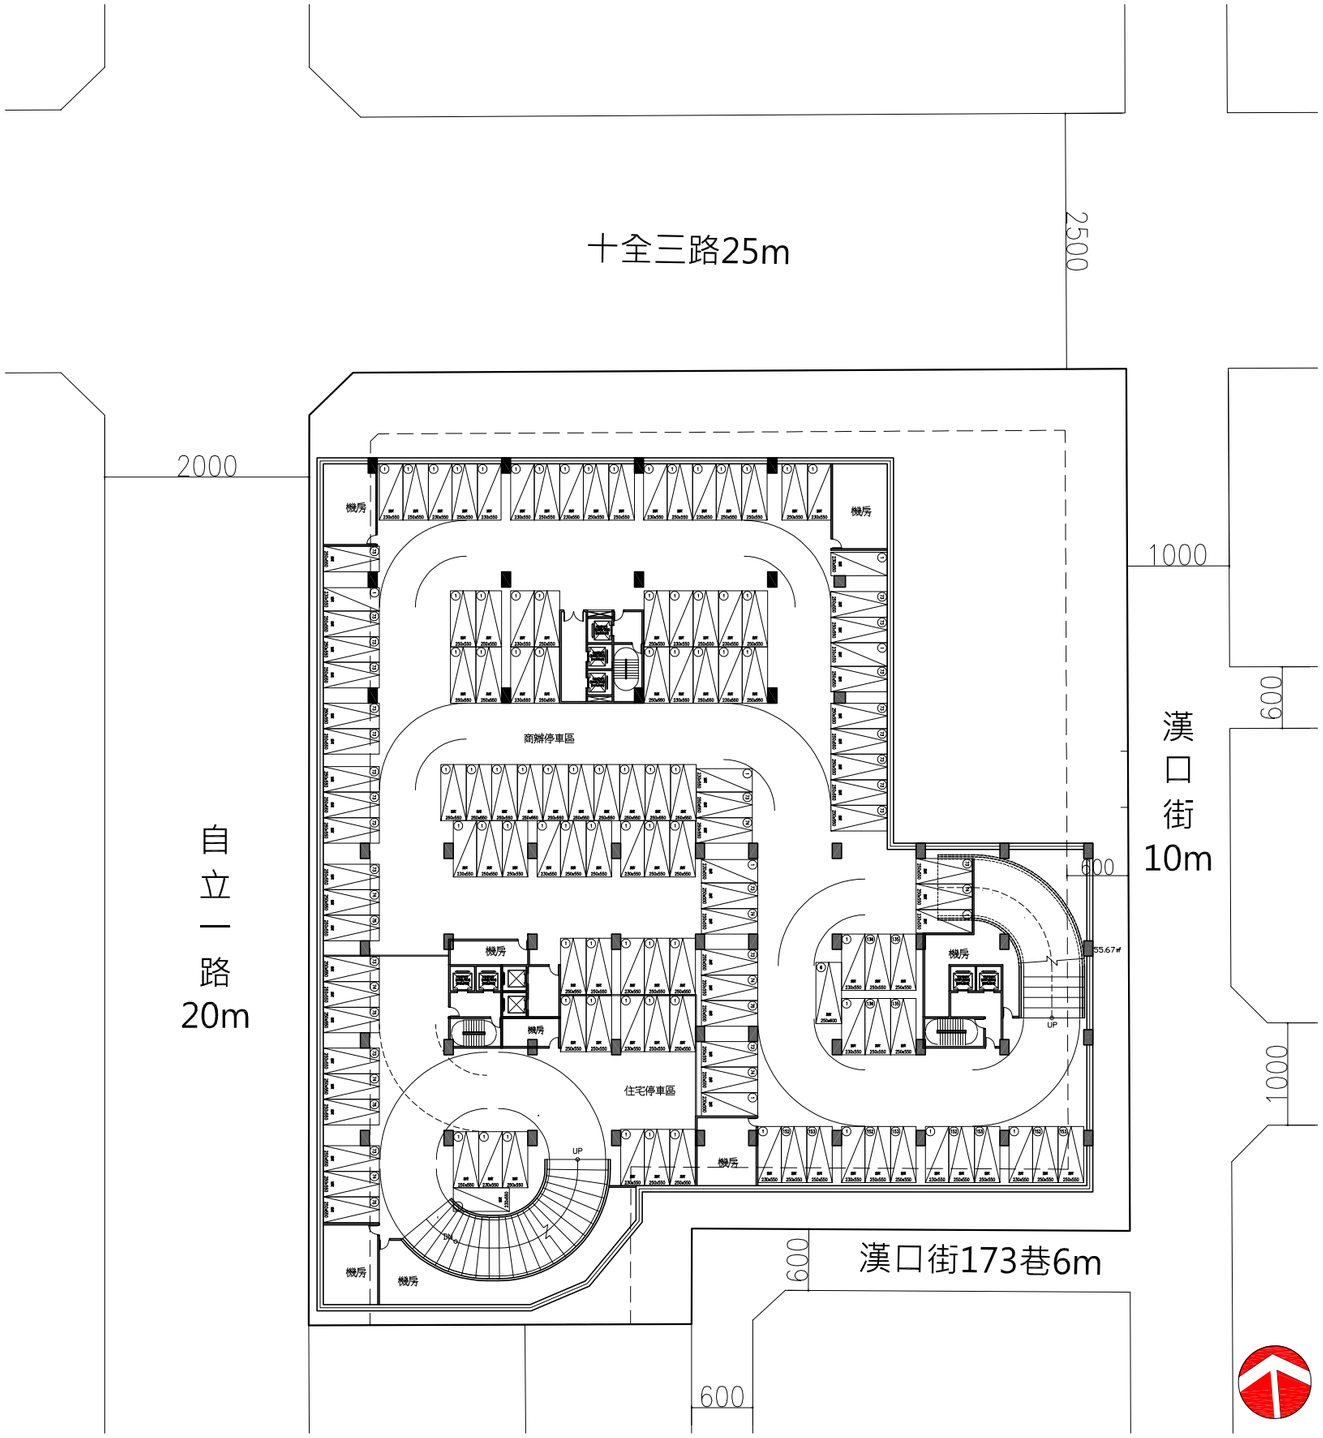

住宅汽車：21台
商辦汽車：116台

合計汽車：137台

高雄市三民區住宅案 Scheme 01　地下三層平面圖S:1/600

李祖原聯合建築師事務所
C.Y.LEE & PARTNERS Architects / Planners

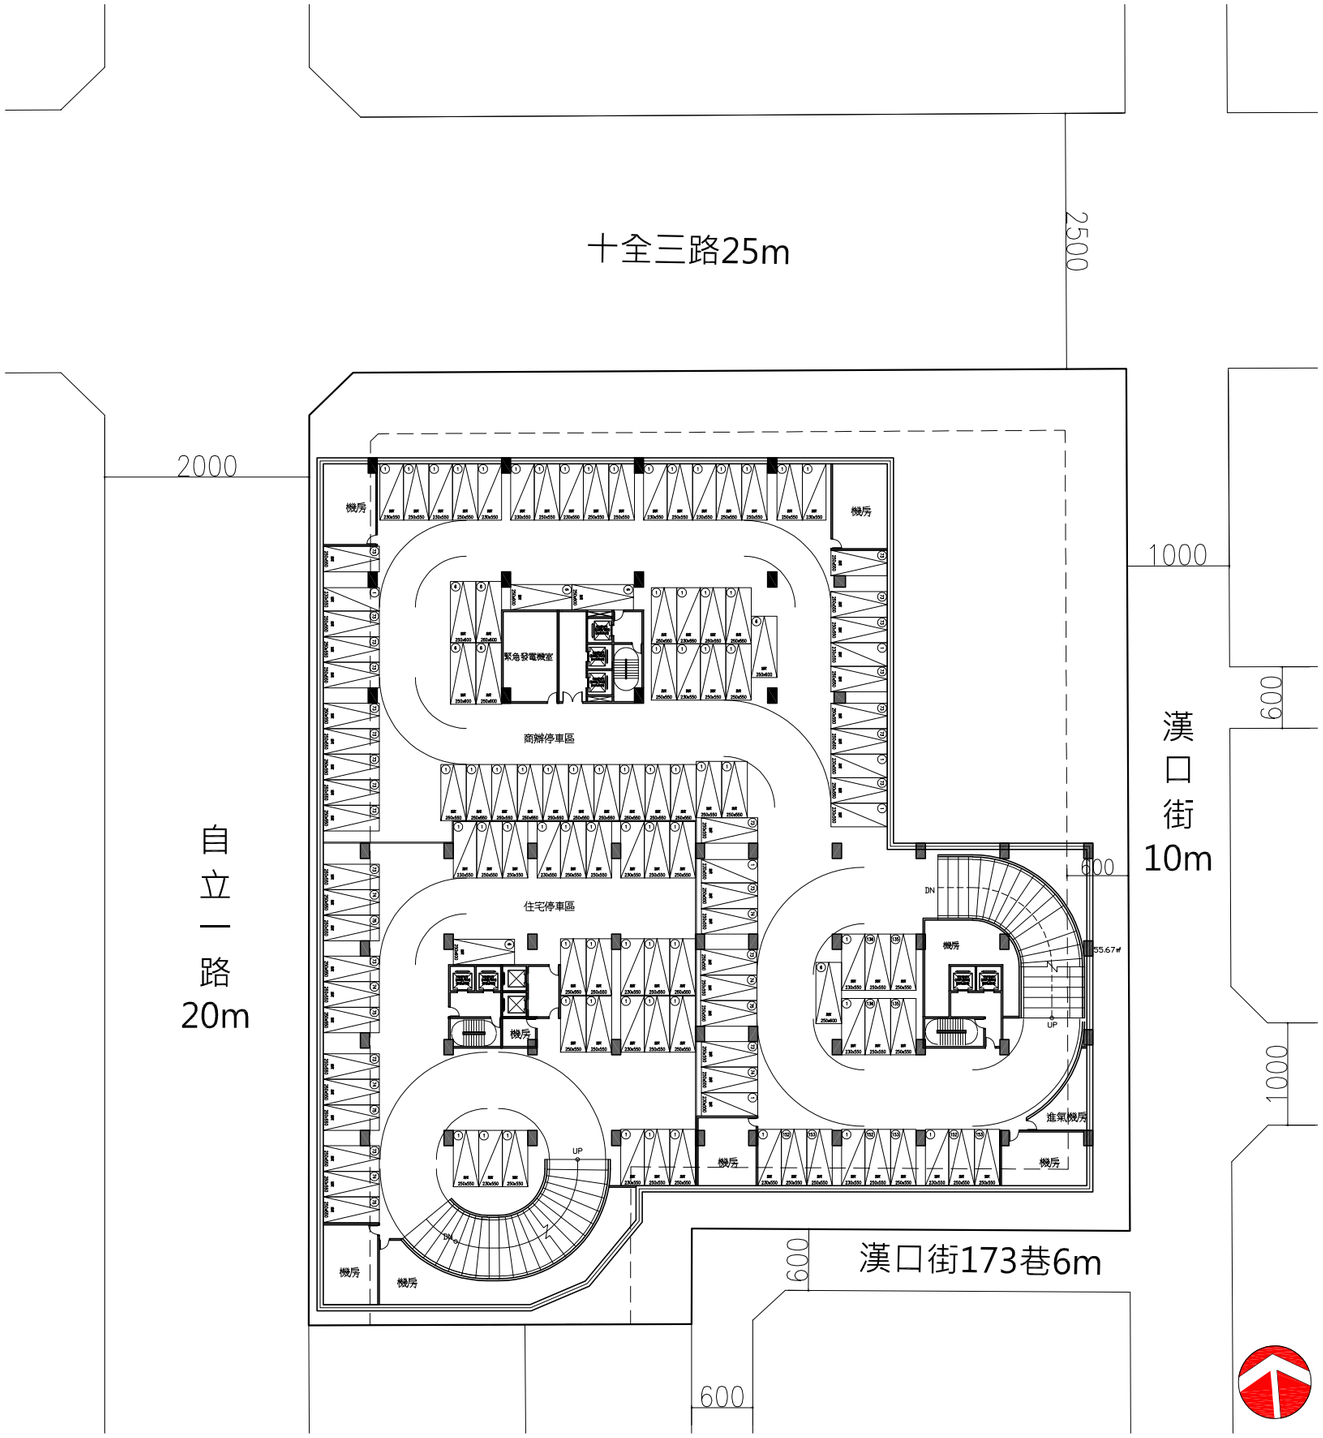

住宅汽車：38台
商辦汽車：90台

合計汽車：128台

高雄市三民區住宅案 Scheme 01

地下二層平面圖S:1/600

李祖原聯合建築師事務所
C.Y.LEE & PARTNERS Architects / Planners

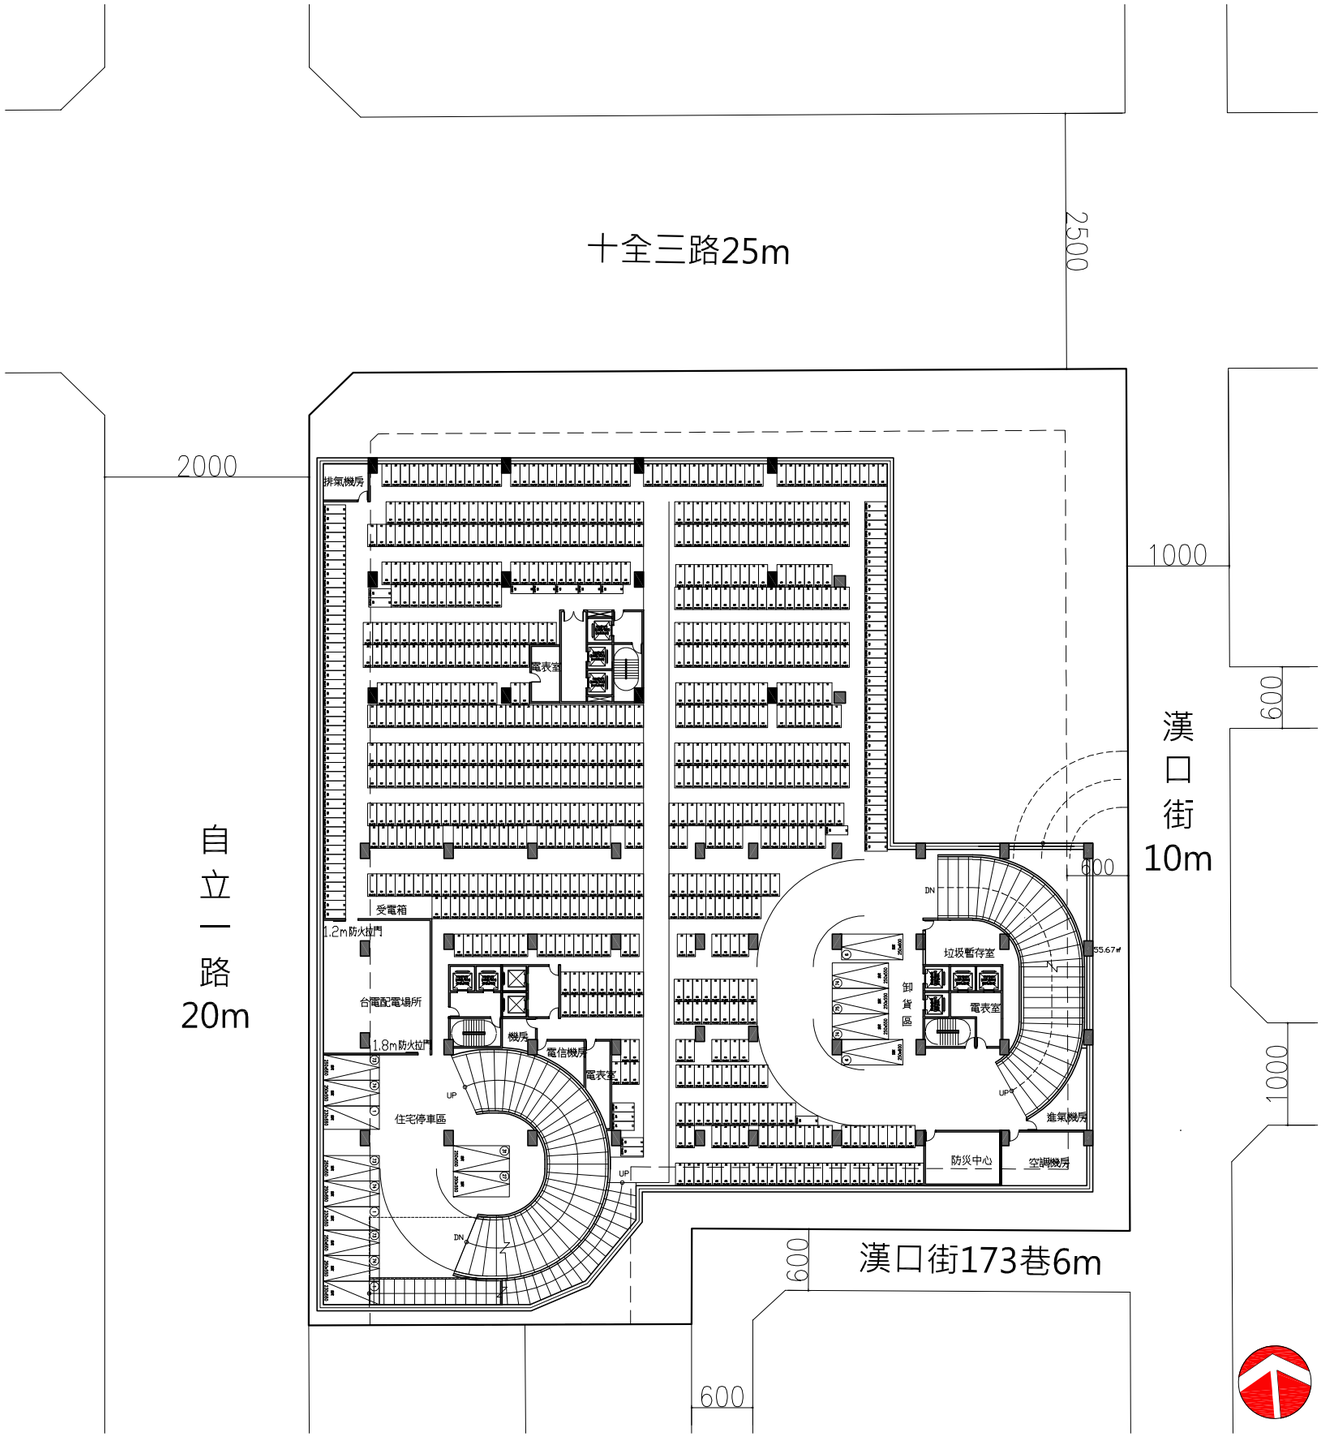

地下一層
住宅汽車：11台
商辦汽車：5台
共16台

機車：876（需 888台）
商辦汽車共：211台（需173台）
住宅汽車共：356台（需300台）
共567台

高雄市三民區住宅案 Scheme 01　地下一層平面圖S:1/600

李祖原聯合建築師事務所
C.Y.LEE & PARTNERS Architects / Planners

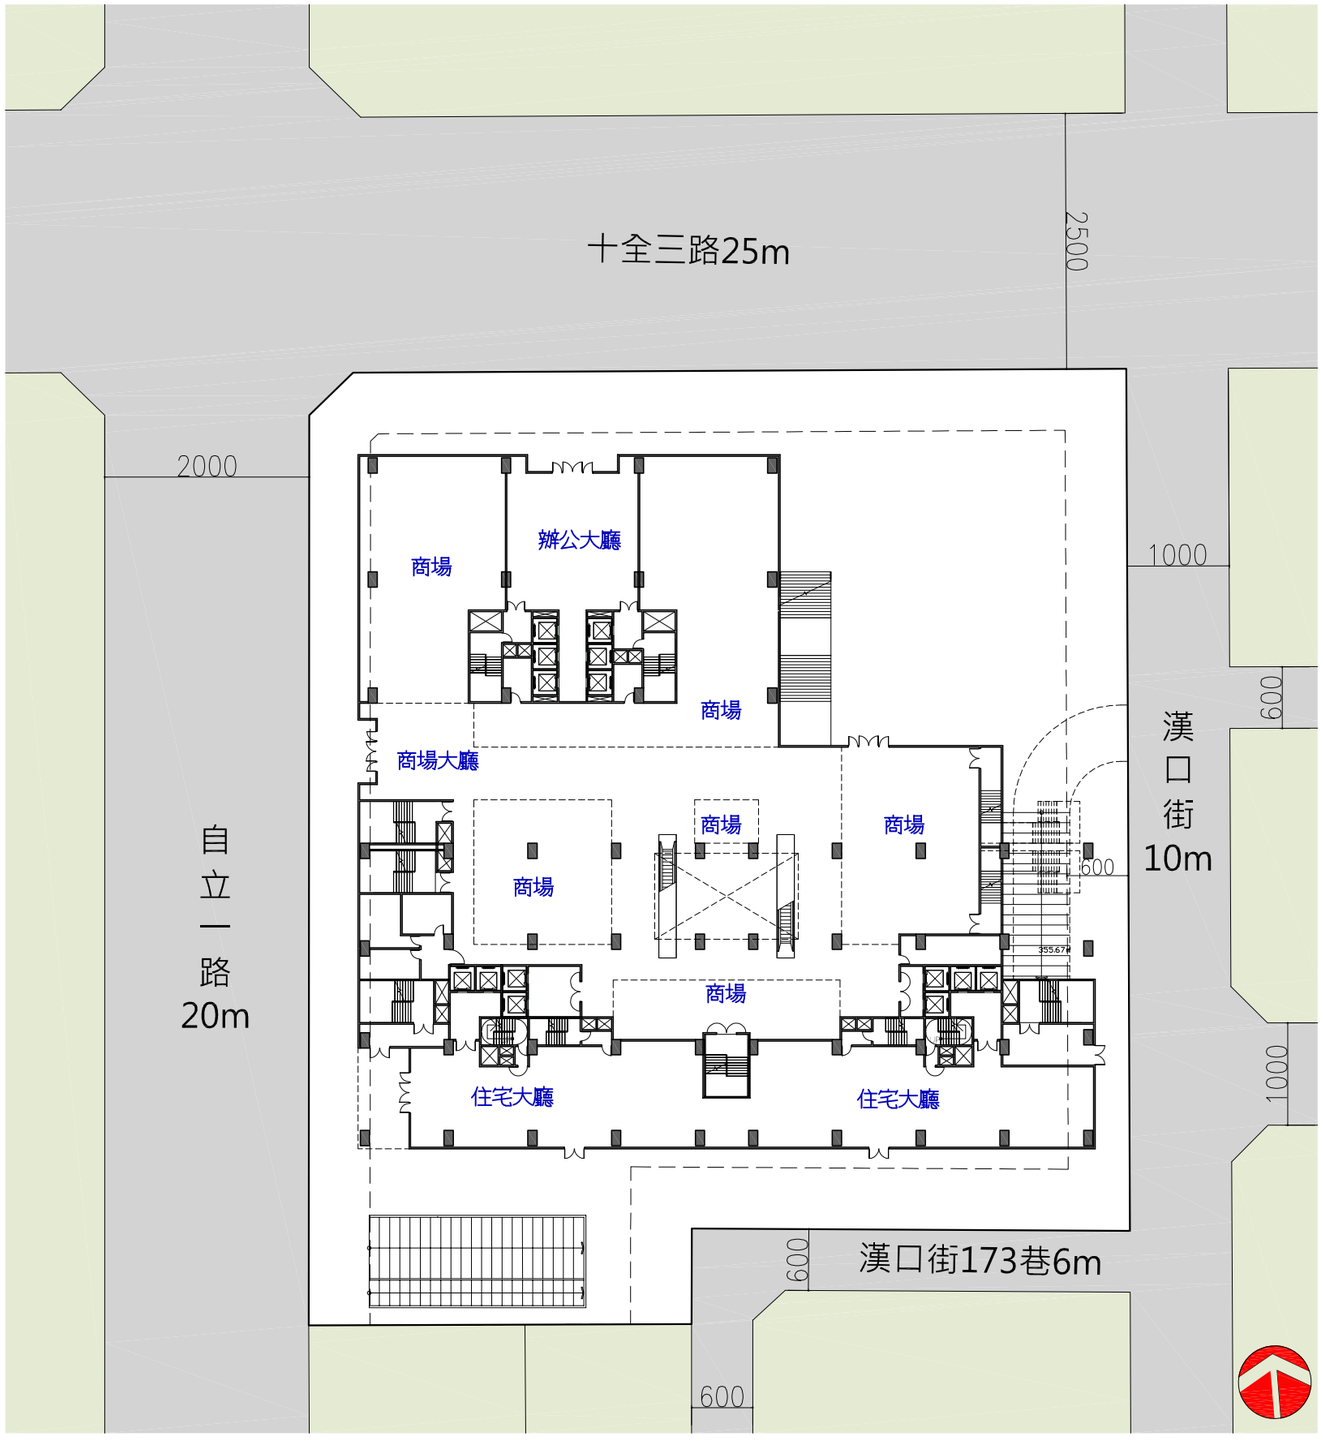

高雄市三民區

	法令分析項次	基本分析 ㎡(坪)			
1	基地面積〈㎡〉	**7,074.00**	〈	**2,139.89**	〉
2	使用分區	商四區	/	商二特區	
	各使用分區面積（㎡）	**4,706.00**	/	**2,368.00**	
3	法定建蔽率	60%	/	50%	
4	法定容積率	630%	/	300%	
5	設計建築面積	4,007.60	〈	1,212.30	〉
6	預估地下室開挖率	70%			
7	預估地下室樓層數	5			
8	危老獎勵容積率 / 容積比	207.81%	/	40.00%	
9	容積移轉容積率 / 容積比	0.00%	/	0.00%	
9	預估設計總容積率	727.35%			
10	基準容積樓地板面積 FA〈㎡〉	36,751.80	〈	11,117.42	〉
11	危老獎勵容積樓地板面積〈㎡〉	14,700.72	〈	4,446.97	〉
12	容積移轉容積樓地板面積 〈㎡〉	0.00	〈	0.00	〉
13	允建容積樓地板面積 ΣFA〈㎡〉【10~12】	**51,452.52**	〈	**15,564.39**	〉
14	高雄厝通用設計容積樓地板面積	**735.04**	〈	**222.35**	〉
15	地下停車空間面積〈㎡〉	24,759.00	〈	7,489.60	〉
16	機電設備面積〈㎡〉ΣFA*15%	5,512.77	〈	1,667.61	〉
17	梯廳面積〈㎡〉(ΣFA+15%機電)×1.075×7.5%	4,652.09	〈	1,407.26	〉
18	屋突面積〈㎡〉建築面積×15%×3	1,803.42	〈	545.53	〉
19	總樓地板面積〈㎡〉【13~18】	88,914.83	〈	26,896.74	〉
20	不含停車空間及屋突樓地板面積〈㎡〉【12,15,18】	62,352.41	〈	18,861.61	〉
21	陽台面積〈㎡〉(ΣFA+15%機電)×1.075×7.5%	4,652.09	〈	1,407.26	〉
22	高雄厝景觀陽台	7,404.35	〈	2,239.82	〉
23	法定汽車位	408			
24	無障礙車位	5			
25	機車位	408			
備註	1、本分析表暫以危老獎勵40%檢討、高雄厝通用設計2%及高雄厝景觀陽台。 2、地下開挖率及樓層數僅供參考。				

- 實設建蔽率: 58.04%
- 實設地上層樓地板:29856.11(住)+21460.98(辦)+11035.32(商)
  =62,352.41 ㎡(不含屋突、地下層)
- 單層樓地板:住宅標準層面積:695+695=1390㎡
  辦公室標準層面積:1000㎡
  商場標準層面積 :4000㎡
- 總 樓 高: 1F:5M , 商場2F-4F=5M/F*3=15M
  住宅 20+5M(5F)+3.4*16+3.6*2=86.6M
  辦公室20+4.2*19=99.8M
- 設計規模: 地下5層 1幢3棟 地上23層住宅、地上23層辦公大樓
  1層 店面、門廳 1-4層 商場
- 停車: 法定機車=617台 實設機車=876台(交評建議)
  法定汽車=408 實設汽車=563台(交評建議473台)

高雄市三民區住宅案 Scheme 01 一層平面圖S:1/600

李祖原聯合建築師事務所
C.Y.LEE & PARTNERS Architects / Planners

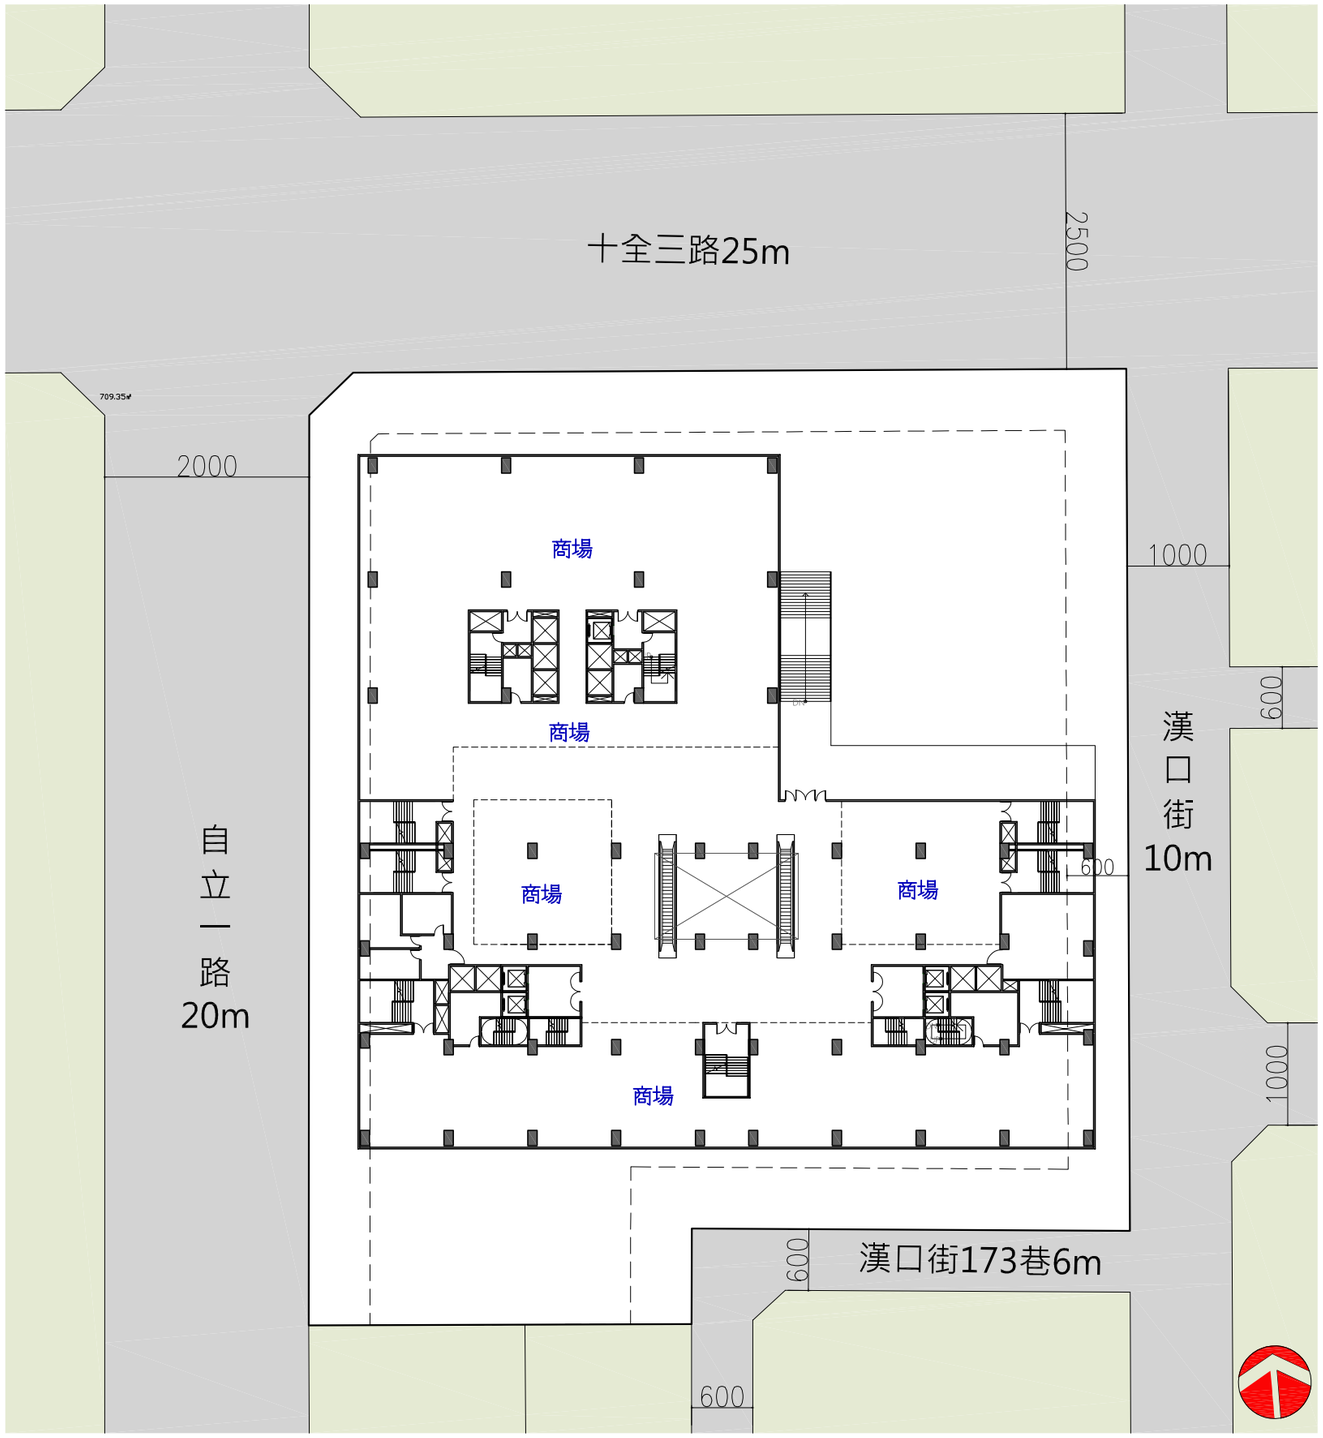

高雄市三民區住宅案 Scheme 01

二層平面圖S:1/600

李祖原聯合建築師事務所
C.Y.LEE & PARTNERS Architects / Planners

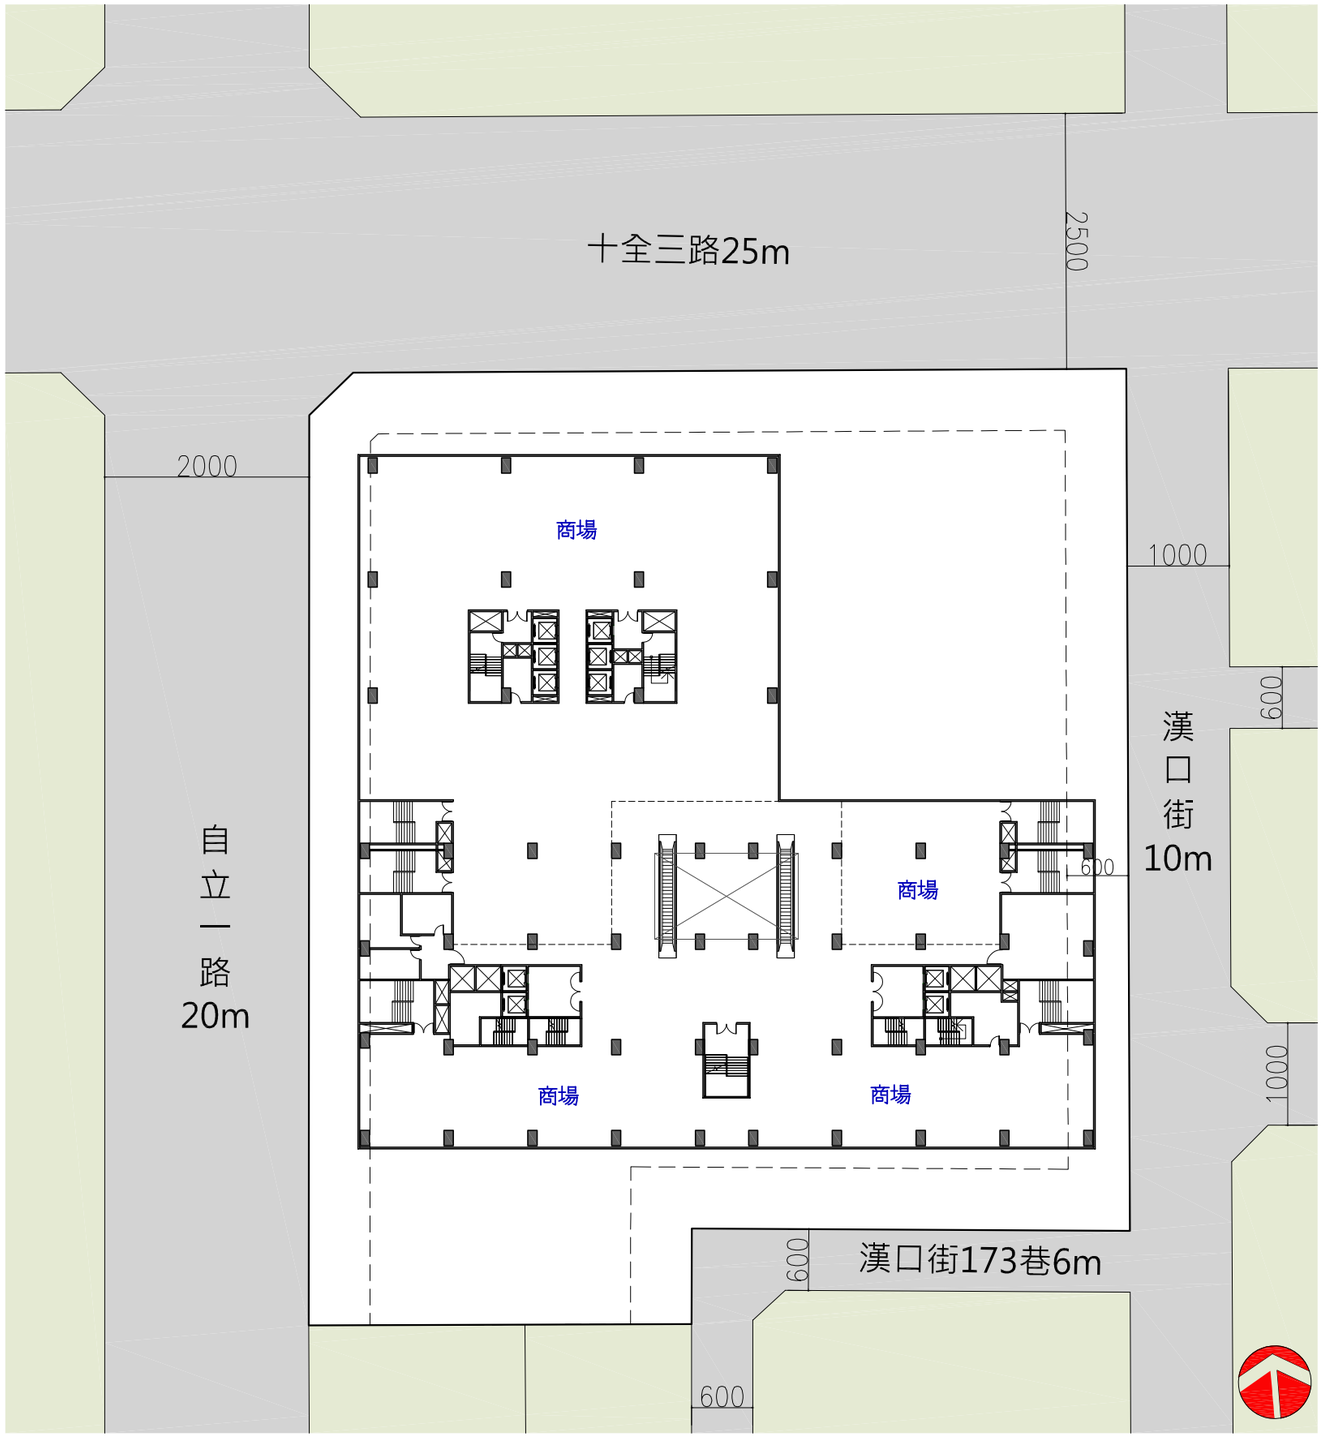

高雄市三民區住宅案 Scheme 01

三至四層平面圖S:1/600

李祖原聯合建築師事務所
C.Y.LEE & PARTNERS Architects / Planners

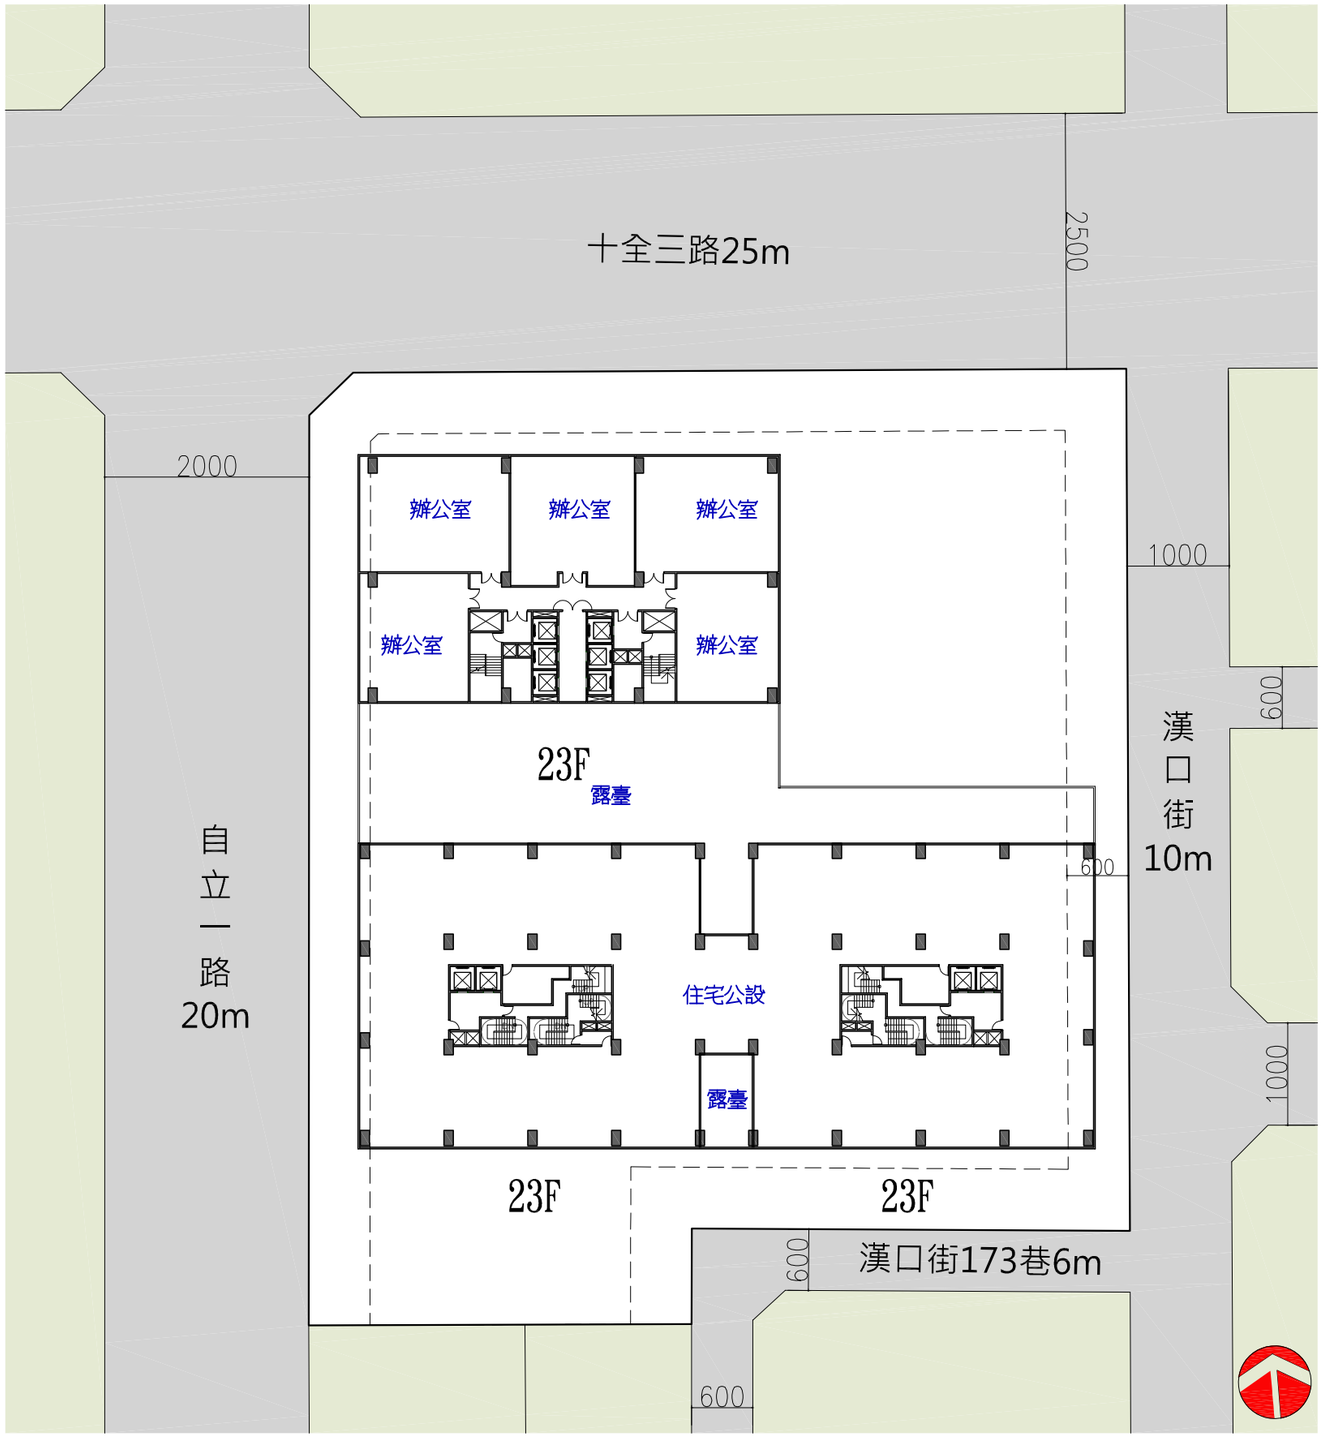

高雄市三民區住宅案 Scheme 01

五層平面圖S:1/600

李祖原聯合建築師事務所
C.Y.LEE & PARTNERS Architects / Planners

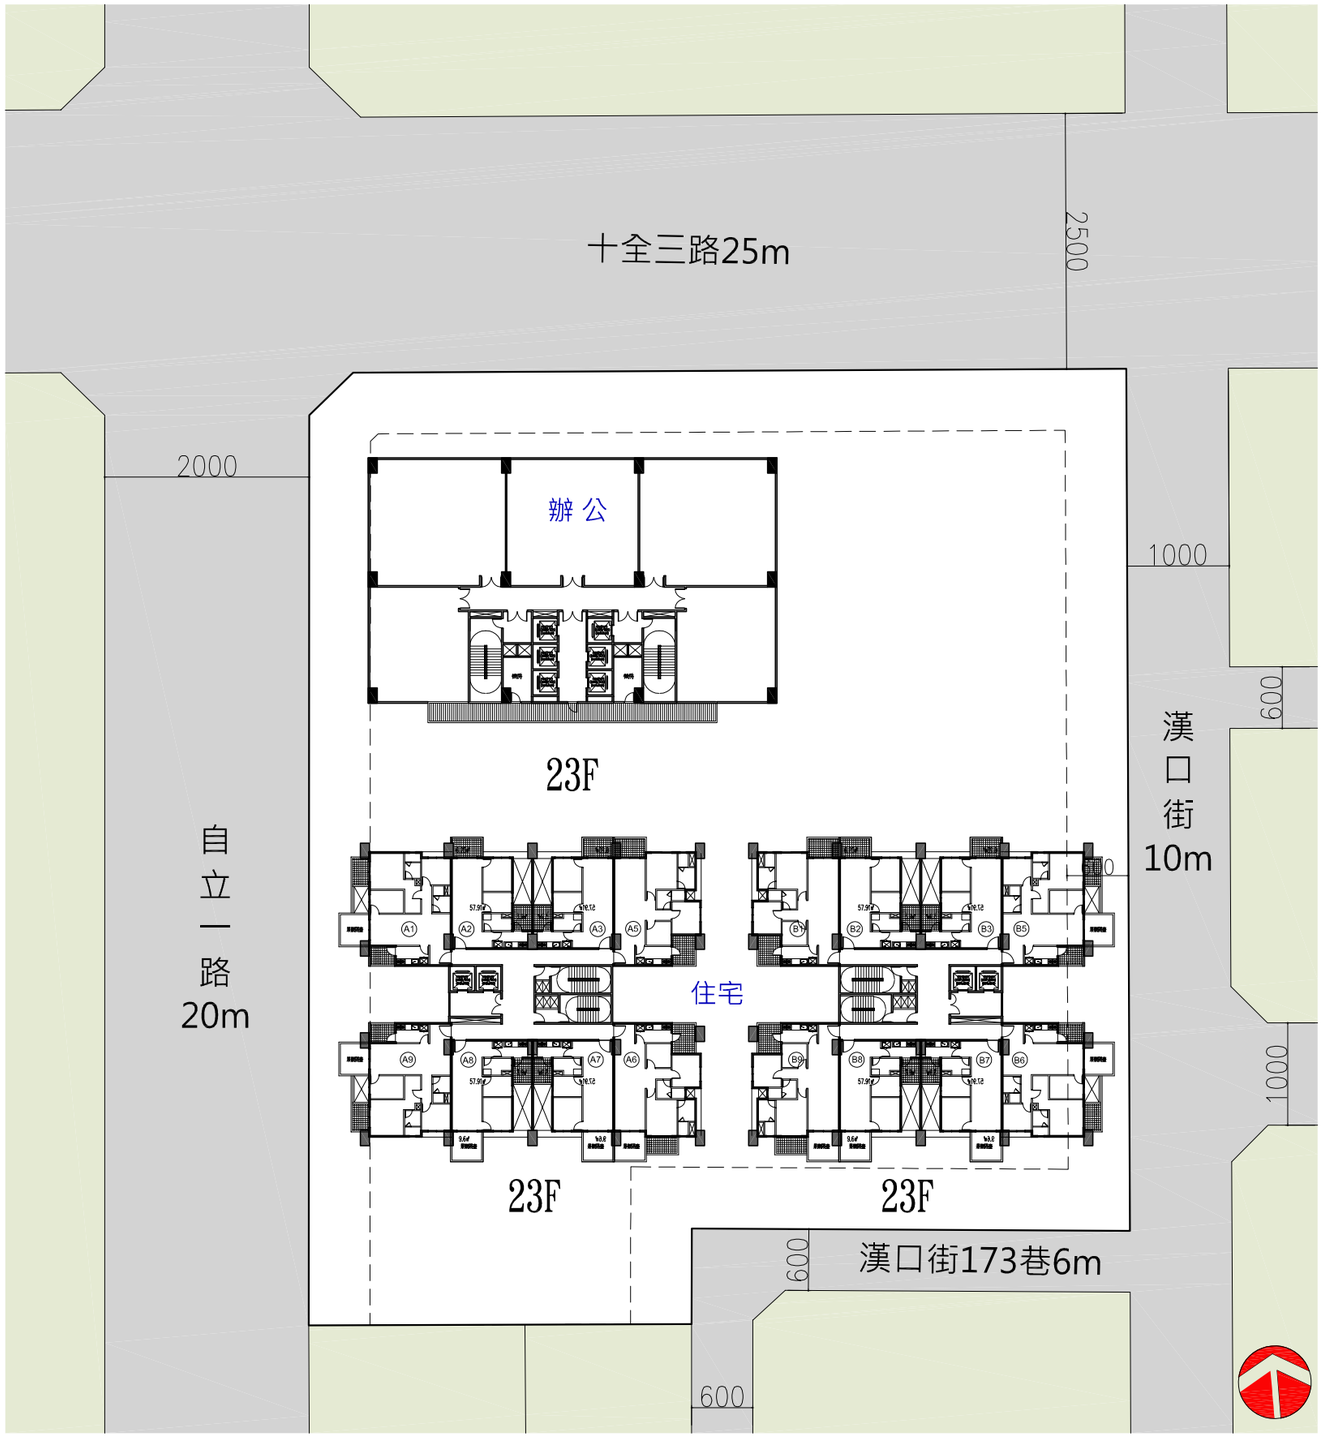

高雄市三民區住宅案 Scheme 01 六至二十三層平面圖S:1/600

李祖原聯合建築師事務所
C.Y.LEE & PARTNERS Architects / Planners

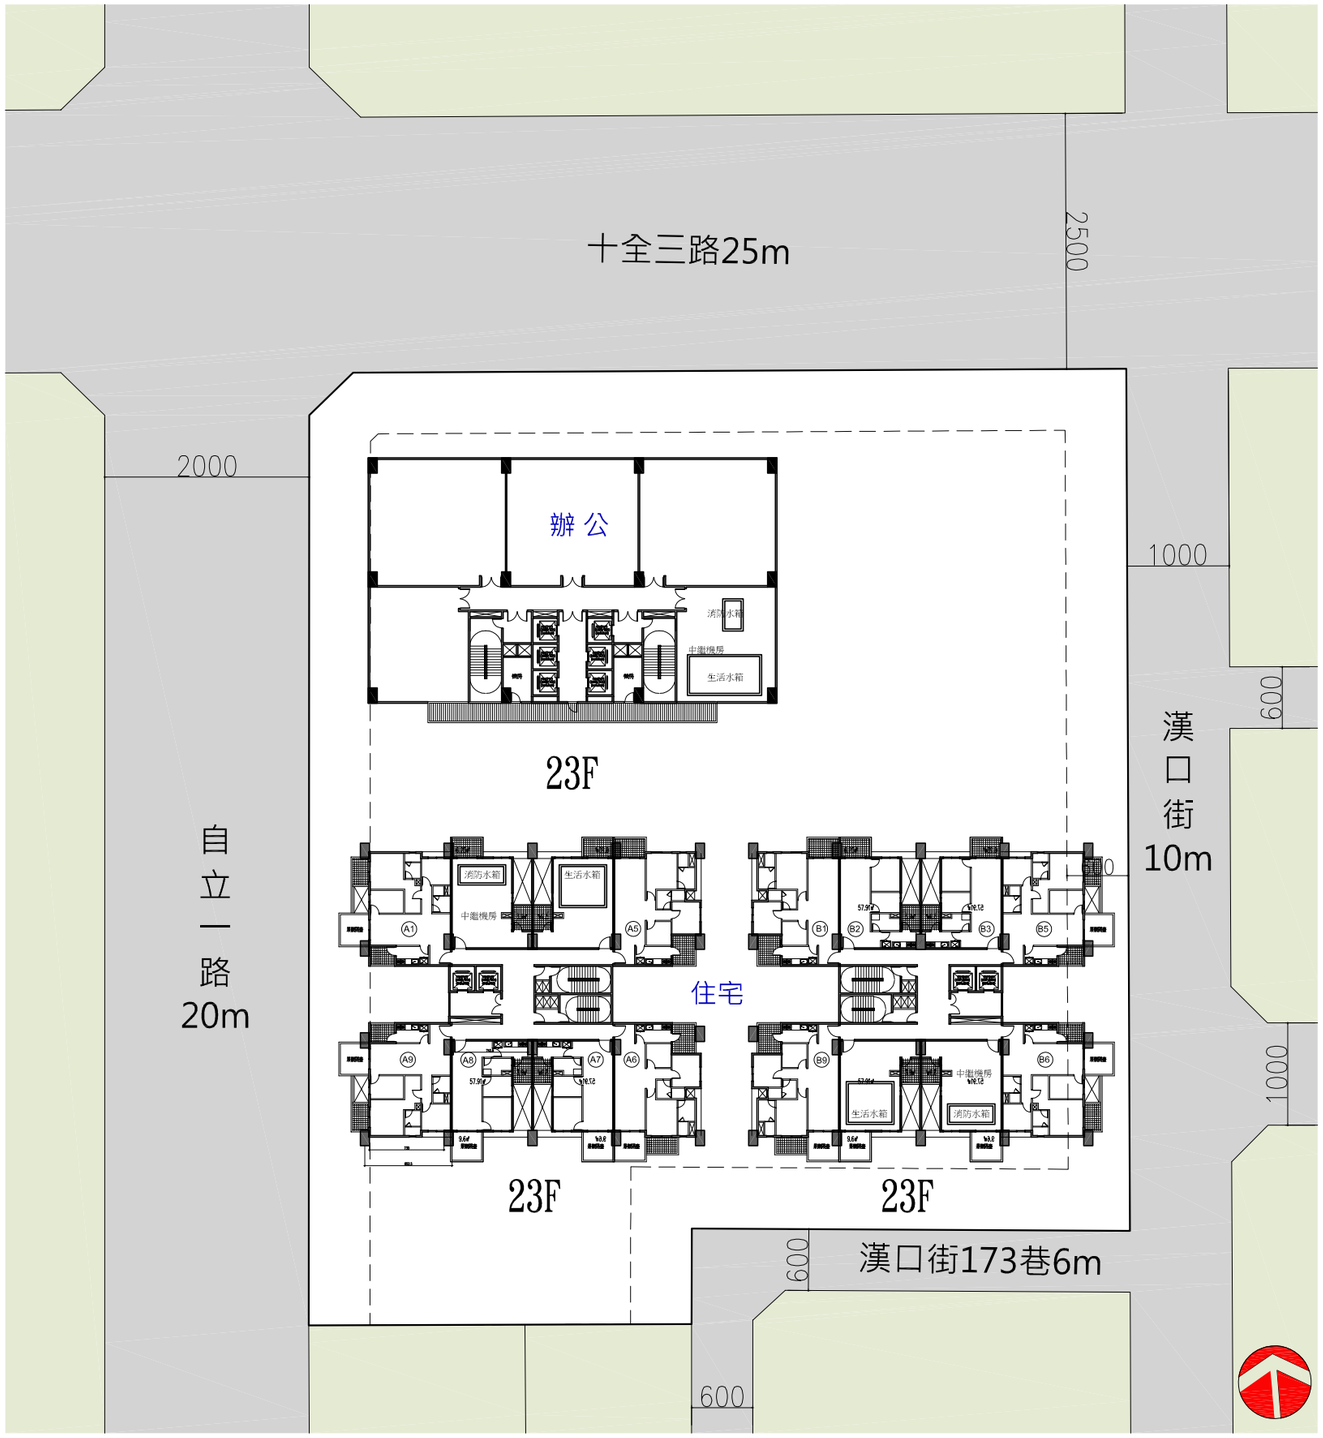

高雄市三民區住宅案 Scheme 01

十三層平面圖S:1/600

李祖原聯合建築師事務所
C.Y.LEE & PARTNERS Architects / Planners