面積計算表

起造人	三嘉營造股份有限公司 負責人：謝順發
土地座落	台南市仁德區崁腳北段820,821,895,900,901,902,905,906,907地號，共9筆(部分)
基地面積	20519.6㎡
使用分區	乙種工業區
私設通路	台南市仁德區崁腳北段820,821,822,823,895,898,899,900,901,902,905,906,907,920地號，崁腳南8地號，共15筆(部分)
建築面積	12973.92㎡
建蔽率	12973.92/20519.6=63.23% < 70% ok!!
容積率	12973.92/20519.6=63.23% < 210% ok!!
法定空地	20519.6x30%=6155.88㎡
建築物高度	11.15m (簷高=9.95m ； 樓層高=9.35m)
樓 層	樓地板面積
壹 層	作業廠房(C-1)：12973.92㎡ (詳分戶表)
總樓地板面積	12973.92㎡
總工程造價	12973.92x5300=68,761,776元

仁德區-崁腳北段ABC棟

戶號		A1	A2	A3	A4	A5	A6	A7	A8	A9	A10	A11	A12	A13	A14	A15	A16	合計
基地面積	㎡	466.93	288.87	289.48	257.93	258.51	259.09	252.66	246.02	245.7	280.71	283.5	285.4	287.3	289.21	291.11	319.5	4601.92
	坪	141.25	87.38	87.57	78.02	78.2	78.37	76.43	74.42	74.32	84.91	85.76	86.33	86.91	87.48	88.06	96.65	1392.06
建築面積	㎡	210.58	188.58	188.58	168.58	168.58	168.58	168.58	168.58	168.58	168.58	168.58	168.58	168.58	168.58	168.58	173.78	2784.48
	坪	63.7	57.05	57.05	51	51	51	51	51	51	51	51	51	51	51	51	52.57	842.37

戶號		B1	B2	B3	B4	B5	B6	B7	B8	B9	B10	B11	B12	B13	B14	B15	B16	B17	B18
基地面積	㎡	334.25	218	218	218	217.95	217.38	216.65	215.93	215.57	217.31	219.4	221.48	223.57	225.66	227.75	229.83	243.02	241.43
	坪	101.11	65.95	65.95	65.95	65.93	65.76	65.54	65.32	65.21	65.74	66.37	67	67.63	68.26	68.89	69.52	73.51	73.03
建築面積	㎡	189.11	150.1	150.1	150.1	150.1	150.1	150.1	150.1	150.1	150.1	150.1	150.1	150.1	150.1	150.1	150.1	154.7	154.7
	坪	57.2	45.41	45.41	45.41	45.41	45.41	45.41	45.41	45.41	45.41	45.41	45.41	45.41	45.41	45.41	45.41	46.8	46.8

戶號		B19	B20	B21	B22	B23	B24	B25	B26	B27	B28	B29	B30	B31	B32	B33	B34	B35	合計
基地面積	㎡	227.79	226.73	226.94	227.21	227.48	227.75	227.97	227.56	226.92	226.3	225.67	225.04	224.41	223.78	223.15	222.52	233.53	7971.93
	坪	68.91	68.59	68.65	68.73	68.81	68.89	68.96	68.84	68.64	68.46	68.26	68.07	67.88	67.69	67.5	67.31	70.64	2411.5
建築面積	㎡	150.1	150.1	150.1	150.1	150.1	150.1	150.1	150.1	150.1	150.1	150.1	150.1	150.1	150.1	150.1	150.1	154.7	5306.31
	坪	45.41	45.41	45.41	45.41	45.41	45.41	45.41	45.41	45.41	45.41	45.41	45.41	45.41	45.41	45.41	45.41	46.8	1605.31

戶號		C1	C2	C3	C4	C5	C6	C7	C8	C9	C10	C11	C12	C13	C14	C15	C16
基地面積	㎡	431.27	279.6	284.4	230.97	234.08	239.26	245.59	251.92	258.25	253.22	229.92	229.92	229.92	229.92	229.92	241.99
	坪	130.46	84.58	86.03	69.87	70.81	72.38	74.29	76.21	78.12	76.6	69.55	69.55	69.55	69.55	69.55	73.2
建築面積	㎡	231.92	198.58	198.58	160.58	160.58	160.58	160.58	160.58	160.58	160.58	160.58	160.58	160.58	160.58	160.58	165.52
	坪	70.16	60.07	60.07	48.58	48.58	48.58	48.58	48.58	48.58	48.58	48.58	48.58	48.58	48.58	48.58	50.07

戶號		C17	C18	C19	C20	C21	C22	C23	C24	C25	C26	C27	合計
基地面積	㎡	335.72	218	218	234.82	225.64	395.16	371.43	406.49	441.54	476.59	522.22	7945.76
	坪	101.56	65.95	65.95	71.03	68.25	119.54	112.36	122.96	133.56	144.17	157.97	2403.6
建築面積	㎡	189.99	150.1	150.1	150.1	150.1	187.6	233.34	236.08	236.08	236.08	242	4883.13
	坪	57.47	45.41	45.41	45.41	45.41	56.75	70.59	71.41	71.41	71.41	73.2	1477.21

圖例

建築線　停車空間　雜項工作物
地界線　新建築物　空地
計劃道路　原有建物　私設通路
現有巷道　樁位

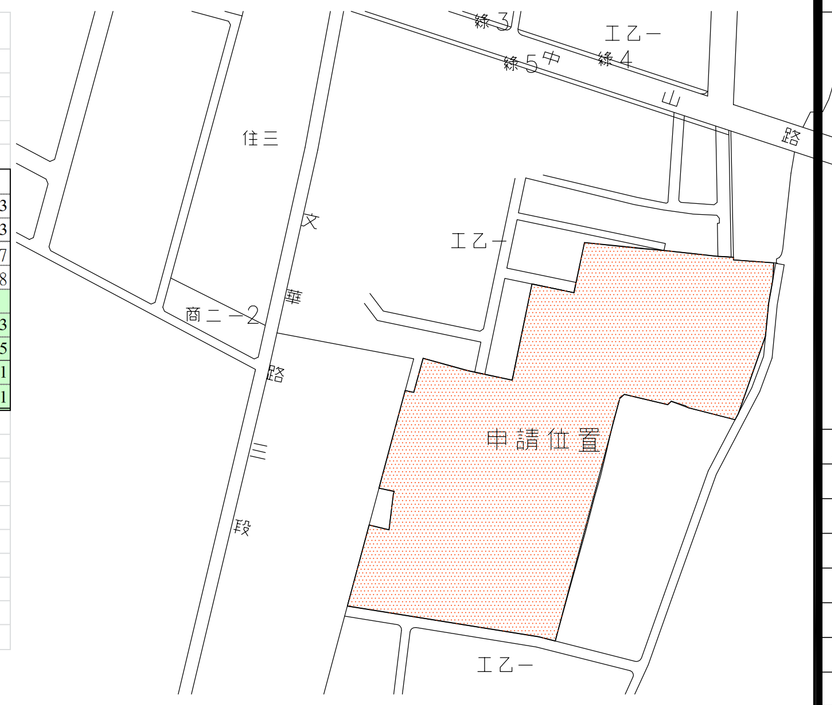

位 置 圖

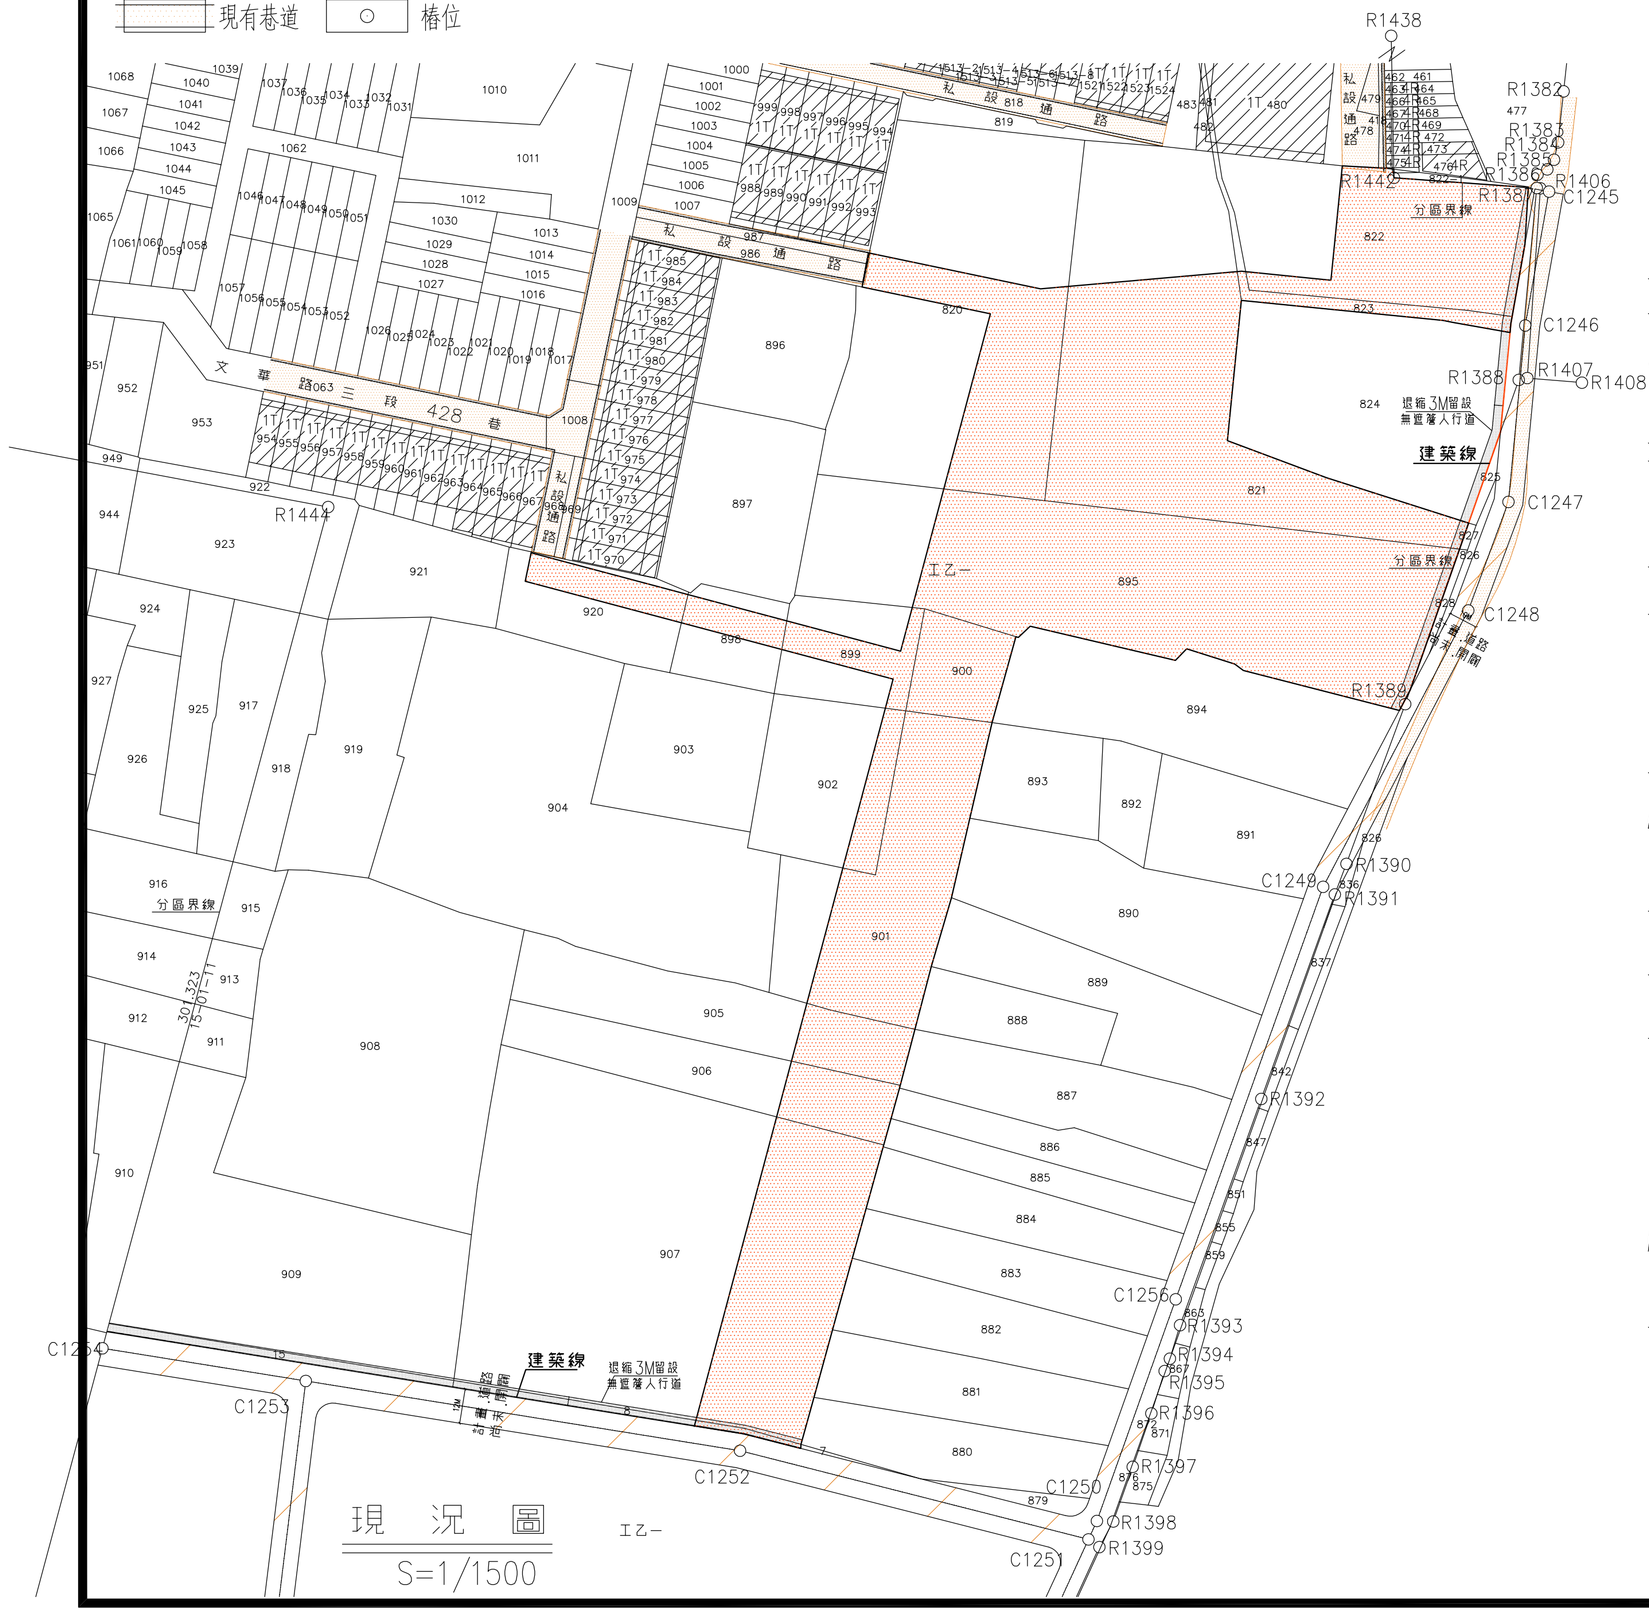

現 況 圖
S=1/1500

地 盤 圖
S=1/1500

附註

版次	修正者	日期	校核	日期	核准	日期

蘇榮林建築師事務所
建築師: 蘇 榮 林
所　址: 高市鳥松區和盛東街15號3F
通訊處: 高市左營區大順一路93號10F之3
TEL:(07)5566099 FAX:(07)5575731
E-mail: archi.su2@msa.hinet.net

審核/

工程名稱/
三嘉營造股份有限公司
作業廠房新建工程

圖名/
面積計算表
位置圖、現況圖，地盤圖

圖檔/

地段/

校核/　核准/

繪圖/　日期/

張號 1/2　圖號 A1 － 1