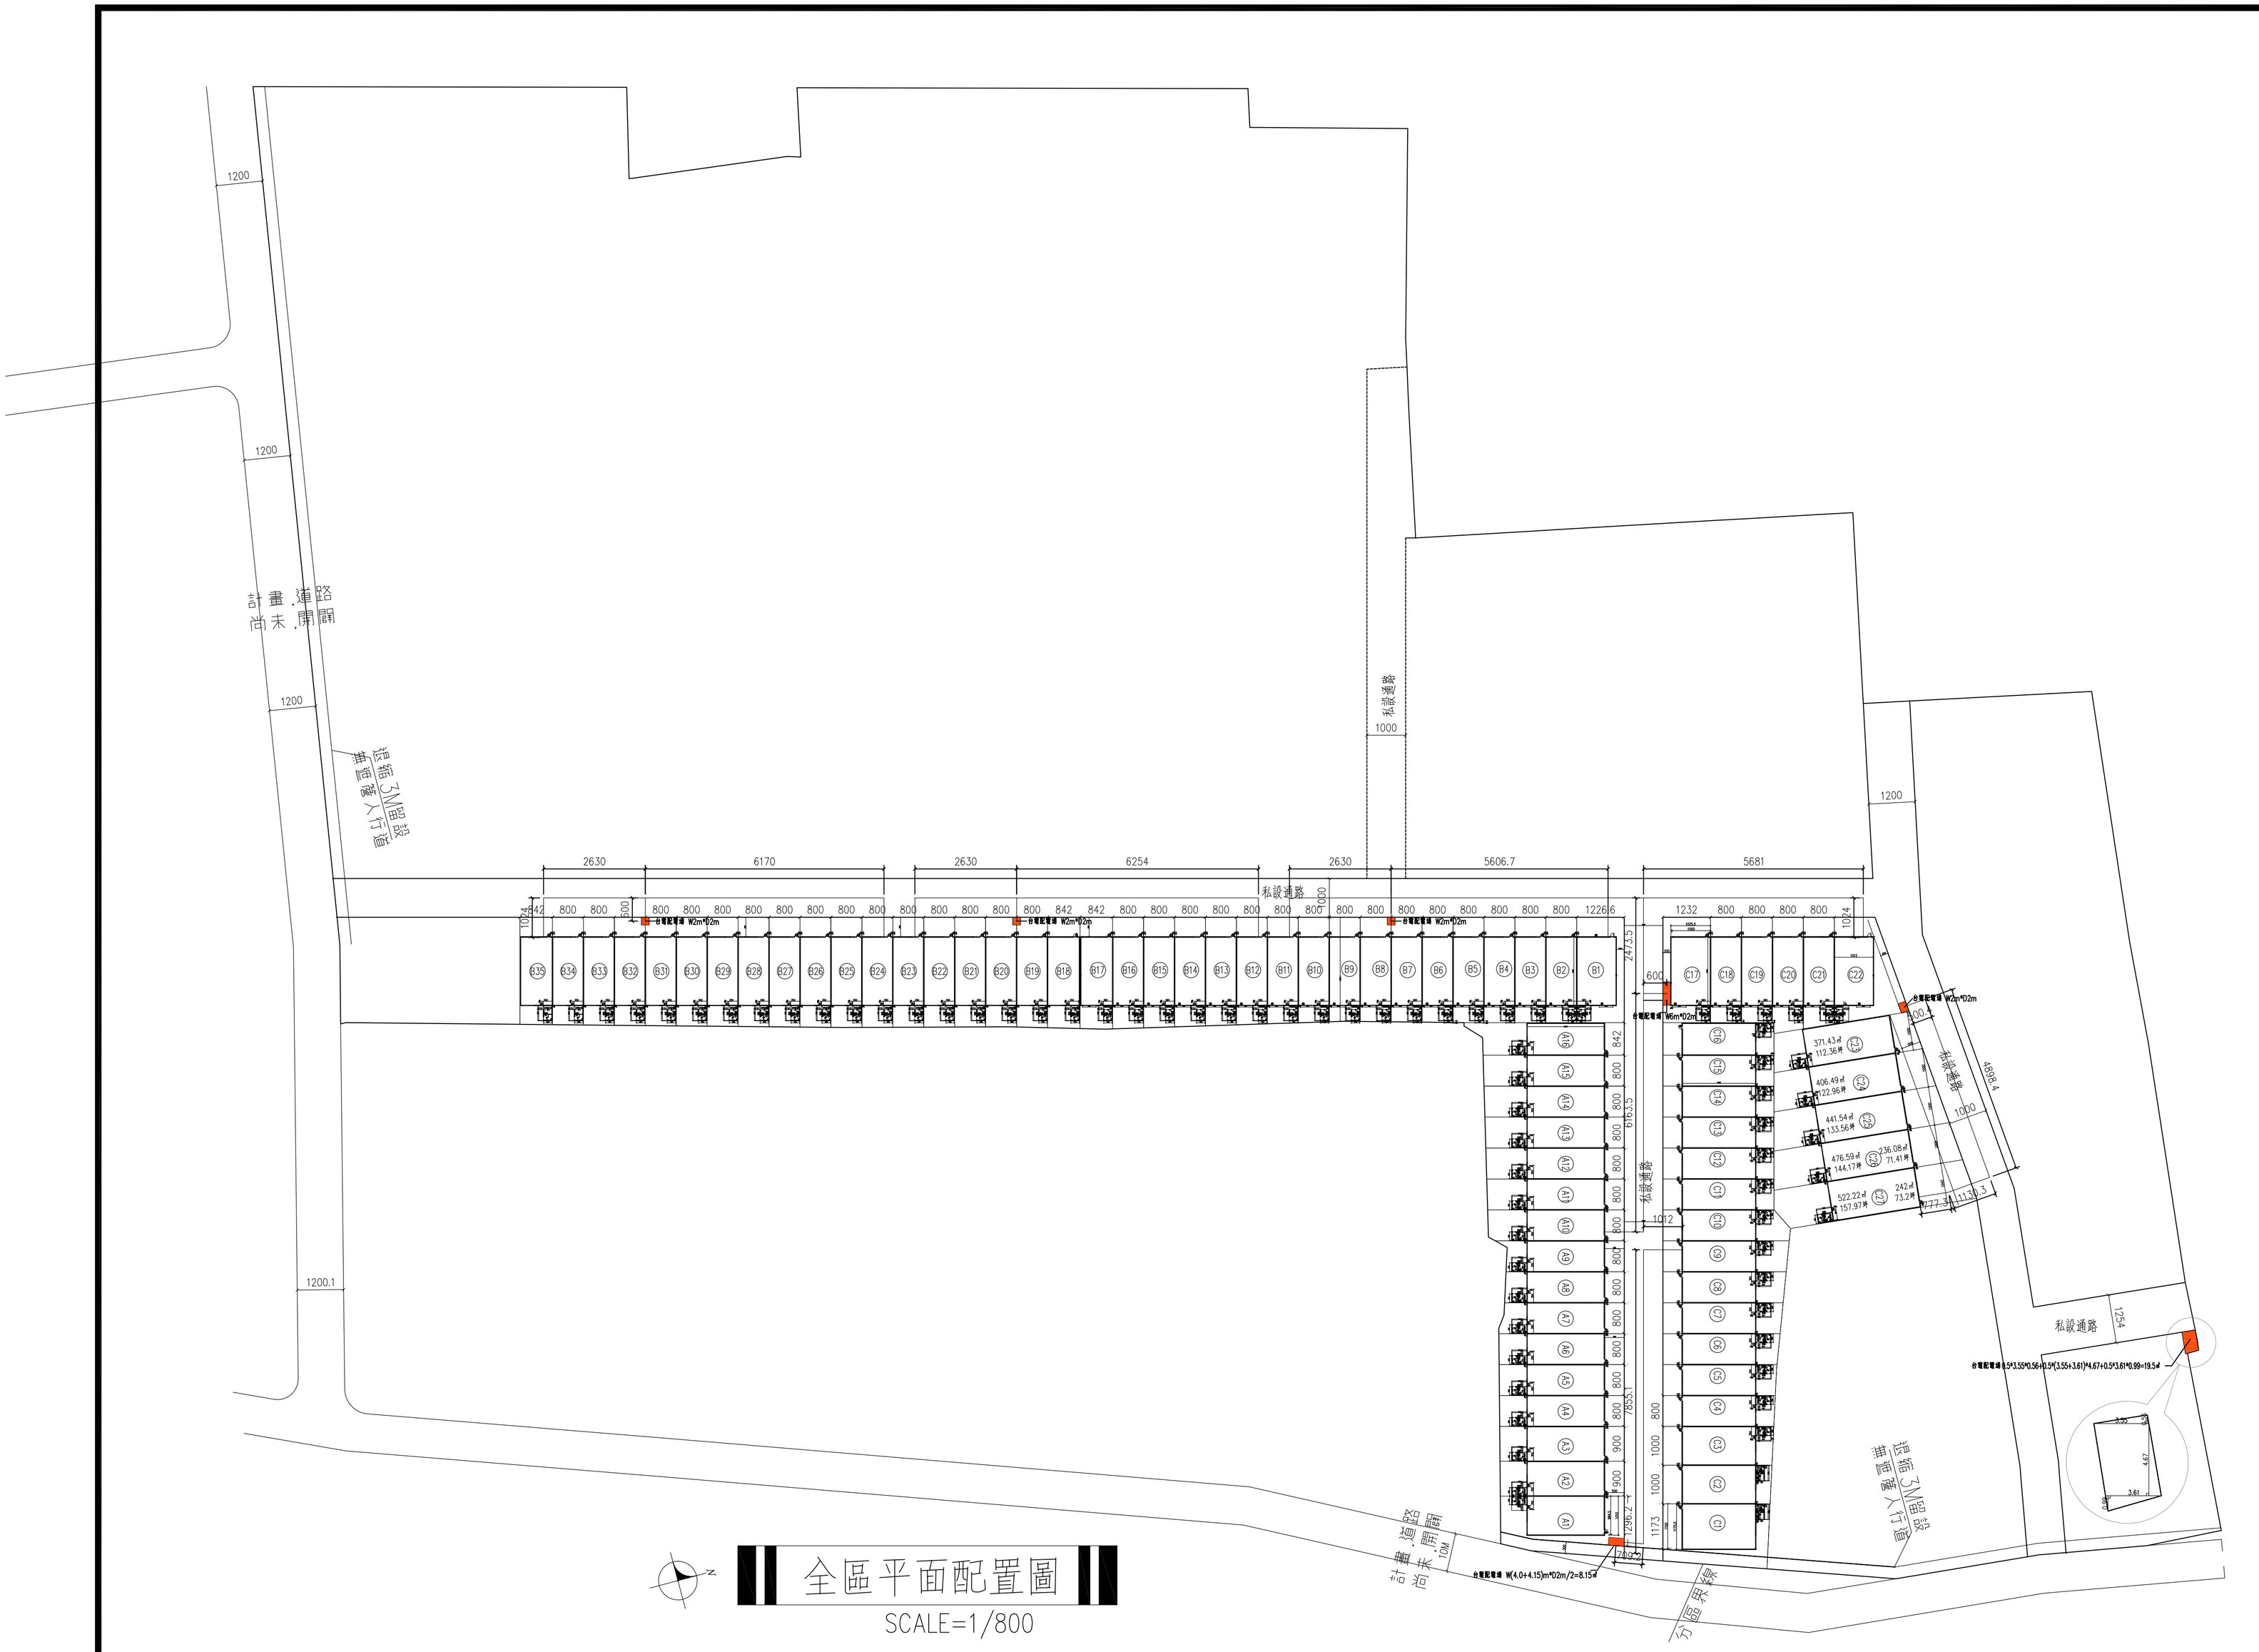

附註

版次	修正者	日/月	校核	日/月	核准	日/月

蘇榮林建築師事務所
建築師: 蘇 榮 林
所　址: 高市鳥松區和盛東街15號3F
通訊處: 高市左營區大順一路93號10F之3
TEL:(07)5566099 FAX:(07)5575731
E-mail: archi.su2@msa.hinet.net

審核/

工程名稱/

三嘉營造股份有限公司
作業廠房新建工程

圖名/

全區平面圖

圖檔/

地段/

校核/　　核准/

繪圖/　　日期/

張號 2/2　　圖號 A1 － 2