關注：原高雄市通盤容積獎勵 1070127~1120126 +1090701防音＋北向日照 之影響

時逢法令變遷/ 請審慎評估

mo

【 高雄市 三民 區 德北4+中華二小 段 4 評估案】 MoAA Case【 SB1 】 2020/1/16

■ 基地位置	15-7=8			筆	都審區	1080328 高雄市都設原則									大樓	B3	＋	15	F	112	戶		
■ 使用分區	住三(3-1)	住三(3-1)	住三(3-1)	區	三民區(三) 1041223（原台鳳製罐廠）										透天	4	1/2	F		0	戶		
■ 建蔽率	50%	50%	50%		50.00%										容積移轉	○	30.00%	30.0%	台鐵三塊厝	暫定			
■ 容積率	240%	240%	240%		240.00%										開放空間	○	20.00%	20.0%	20.00%	暫定			
■ 基地面積	2181.19	0.00	0.00	㎡	2181.19	㎡	659.81	坪							公服空間	○	0.00%	0.00%					
■ 保留地面積(暫定)	0.00	0.00	0.00	㎡	0.00	㎡	0.00	坪							通用空間	×	0.00%	0.00%	0.00%	暫定			
■ 設計基地面積	2181.19	0.00	0.00	㎡	2181.19	㎡	659.81	坪							景觀陽台	×	0.0%	0.0%					
■ 騎樓地 a(未優待)	0.00	0.00	0.00	㎡	Sa1	0	Ba1	0	Sa2	0	Ba2	0	Sa3	0	Ba3	0	透天1	0	透天11	0			
■ 騎樓地 b(優待式)	0.00	0.00	0.00	㎡	Sb1	0.00	Bb1	0.00	Sb2	0	Bb2	0	Sb3	0	Bb3	0	透天2	0	透天21	0			
■ 允建面積	1090.60	0.00	0.00	㎡	1090.60	㎡									大樓	1090.60	透天	0	免計	0			

容積樓地板

■ F A			5234.86	-	0.00	㎡									大樓	5234.86	㎡	透天	0.00	㎡			
■ F A I	=	30.0%	FA	1570.46	㎡	≦0.3FA	聯席案	○	預審會						法定車位	300	150	45.34	63	85次			
■ △F AU	=	1.7%	FA	90.00	㎡		高層建築	×	49.95	≧	50m				容積增額法車位			17.45		50%			
■ △F A(通用)	=	0.0%	≦2%FA	0.0	㎡	≦200	高層結構外審	×	49.95	≧	50m				實設車位			103		56			
■ △F A1	=	20.0%	FA	1046.97	㎡	≦0.2FA	開挖結構外審	○	13.70	≧	12m				汽車位／大樓戶數	103	／	112	＝	92%			
■ △F A2	=	0.0%	FA	0.00	㎡		勞檢危評	×	13.70	≧	18m				機車位／大樓戶數	112	／	112	＝	100%			
■ 梯廳 8.6%	檢核	(0.86)		844.90	㎡	增額	0	中繼層	×	＞	60m	90m			1F室內汽車位	0		BF室內機車位		80			
■ 機電管委	檢核	(209.47)		1020.80	㎡	15%損耗	0	交通評定	126	≧	150	360			1F室外汽車位	0		1F室外機車位		0			

總樓地板及附屬建物

●ΣF A				9807.98	㎡	大樓允用	9807.98	㎡							大樓實設	9807.98	㎡	透天實設	0.00	㎡			
●騎 樓				0.00	㎡		0.00	坪							大樓	0	㎡	透天	0	㎡			
●地下室（法）	80%	(B3)	68.00%	（實）	4449.63	㎡	1346.01	坪										透天停車	0.00	㎡			
●屋突		(3F)			251.33	㎡	76.03	坪							透天	25	＊	0	戶=	0	㎡		
■陽台實	6.38%		損耗	40.3	625.44	㎡	189.19	坪							透天	24	＊	0	戶=	0	㎡		
■景觀陽台	0.00%	0.0%	FA		0.00	㎡	0.00	坪															
■雨遮實	0.00%				0.00	㎡	0.00	坪							高層總樓/空地	7852.28	／	#####	＝	5.32	15/30		

區分建坪/區分售坪

■透天建坪				0.00	㎡		0.00	坪							■透天平均地坪		#DIV/0!	坪	＊	0	戶		
■透天售坪				0.00	㎡		0.00	坪							■透天平均建坪		#DIV/0!	坪	＊	0	戶		
■大廈建坪(實設)			49.8	14508.94	㎡		4388.96	坪							大廈建坪/大廈基地		6.65						
■大廈售坪(實設)				15094.11	㎡		4565.97	坪							大廈售坪/大廈基地		6.92						
● 1+V店鋪 住宅			3665.91	0.00	坪	0	戶	(公設	27.00%	)					地上總坪/全基地		4.88						
●集合住宅				3665.91	坪	112	戶	(公設	35.00%	)					設定公設	35.00%	吸收坪	-0.00					
●車位（汽車＋機車）				900.05	坪	平面式	55	部 (	12.26	坪/部)					法定機車	FALSE	97	FALSE	部				
■損耗建坪	=	0.0%	FA	0.00	㎡	0.00	坪	機械二層	0	部 (	7.35	坪/部)			增設機車	15	自行車位	FALSE	部				
■損耗售坪	=	0.8%	FA	40.28	㎡	12.18	坪	機械三層	48	部 (	4.60	坪/部)			機車總計	112	部 (	0.00	坪/部)				

全基地總建坪/總售坪

雨遮約計當層樓地板 0.00%

理論	■全基地總建坪			14508.95	㎡		4388.96	坪							全基地總建坪/全基地		6.65						
	■全基地總售坪			15134.38	㎡		4578.15	坪							全基地總售坪/全基地		6.94						
實設	■全基地總建坪			14508.94	㎡		4388.96	坪							全基地總建坪/全基地		6.65						
	■全基地總售坪			15094.11	㎡		4565.97	坪							全基地總售坪/全基地		6.92						

全基地本益概算 【 SB1 】

■營建坪平均費用約= 1.15 萬 / 建坪

土建	土地	659.81	×	0.00	萬	＋	0.00	坪	×	0.00	萬	＋	0.00	坪	×	0.00	0	0					
	營建	透天建坪	0.00	坪	×	0.00	萬	大樓地上建坪	3042.9	坪	×	0.00	萬				0						
		景觀陽台	0.00	坪	×	0.00	萬	大樓地下建坪	1346.0	坪	×	0.00	萬										
土融	土融	0	×	50%	×	3.20%		×	2.00	年							0	50%	0				
建融	建融	0	×	50%	×	3.20%		×	1.00	年							0	50%	0				
管銷成本	總銷	0	萬	×	14.00%												0	自備款	0	5,052	萬		
自行車站	應設未設汽車位	＝	56	-	103	(47.4)	10	1.9	0	組	×	78.0	＝				0						
高雄厝回饋	0.00	×	77,212	/	240.00%		×	0.25	×	100%	㎡*元						0.0						
送出基地	2181.19	×	77,212	＋	0.00	×	0	＋	0.00	×	0	㎡*元					5052.4						
	接受基地平均現值=	77,212	道路總現值=	50,524,389	用地取得費率=	100.00%																	
總銷	透天店面	0	戶	×	0	萬	景觀陽台	0.00	坪	×	0.0	萬					0	0	萬				
	1+V店鋪 住宅	0.00	坪	×	0.0	萬	大樓住宅	3665.91	坪	×	0.0	萬					0						
	平面車位	55	部	×	0	萬	機械參車位	48	部	×	0	萬					0						
	機械雙車位	0	部	×	0	萬	機車位	112	部	×	0	萬					0						
ROI	利潤 / 土地款						#DIV/0!										(5,052)	萬					
	利潤 / 自備款						#DIV/0!																
說明	依[	容移	30.0%	開放空間	20.00%	通用空間	###	H =(	3.35	+	3.00	)	+	9	*	3.05	1FL	0.10	B1F	3.30	B2F	3.00	B3F 4.50	B4F 0.00
		公服空間	0.00%	景觀陽台	0.00%	] =	50.00%	+	5	*	3.15	+	0.4	=	49.95			B5F	0.00	B6F	0.00	地梁 2.80	PC 0.10
	1070127~1120126五年獎勵條件或有變化,惠請預估風險!							2R	: 3R :	4R	=	25%	:	75%	:	0%	開挖	13.70					

● MoAA 張文懋建築師事務所 ●高雄市三民區博愛一路366號11F ●電話(07)312-8808 ●傳真(07)312-8809

地籍圖謄本

三民電謄字第145202號

土地坐落：高雄市三民區德北段4,5,7,8,8-1,8-2,9,10,11,12-1,13,14,15地號共13筆

本謄本與地籍圖所載相符（實地界址以複丈鑑界結果為準）

北

資料管轄機關：　高雄市政府地政局三民地政事務所

本謄本核發機關：　高雄市政府地政局三民地政事務所　　主任：黃瓊慧

中　華　民　國　108年10月03日14時04分

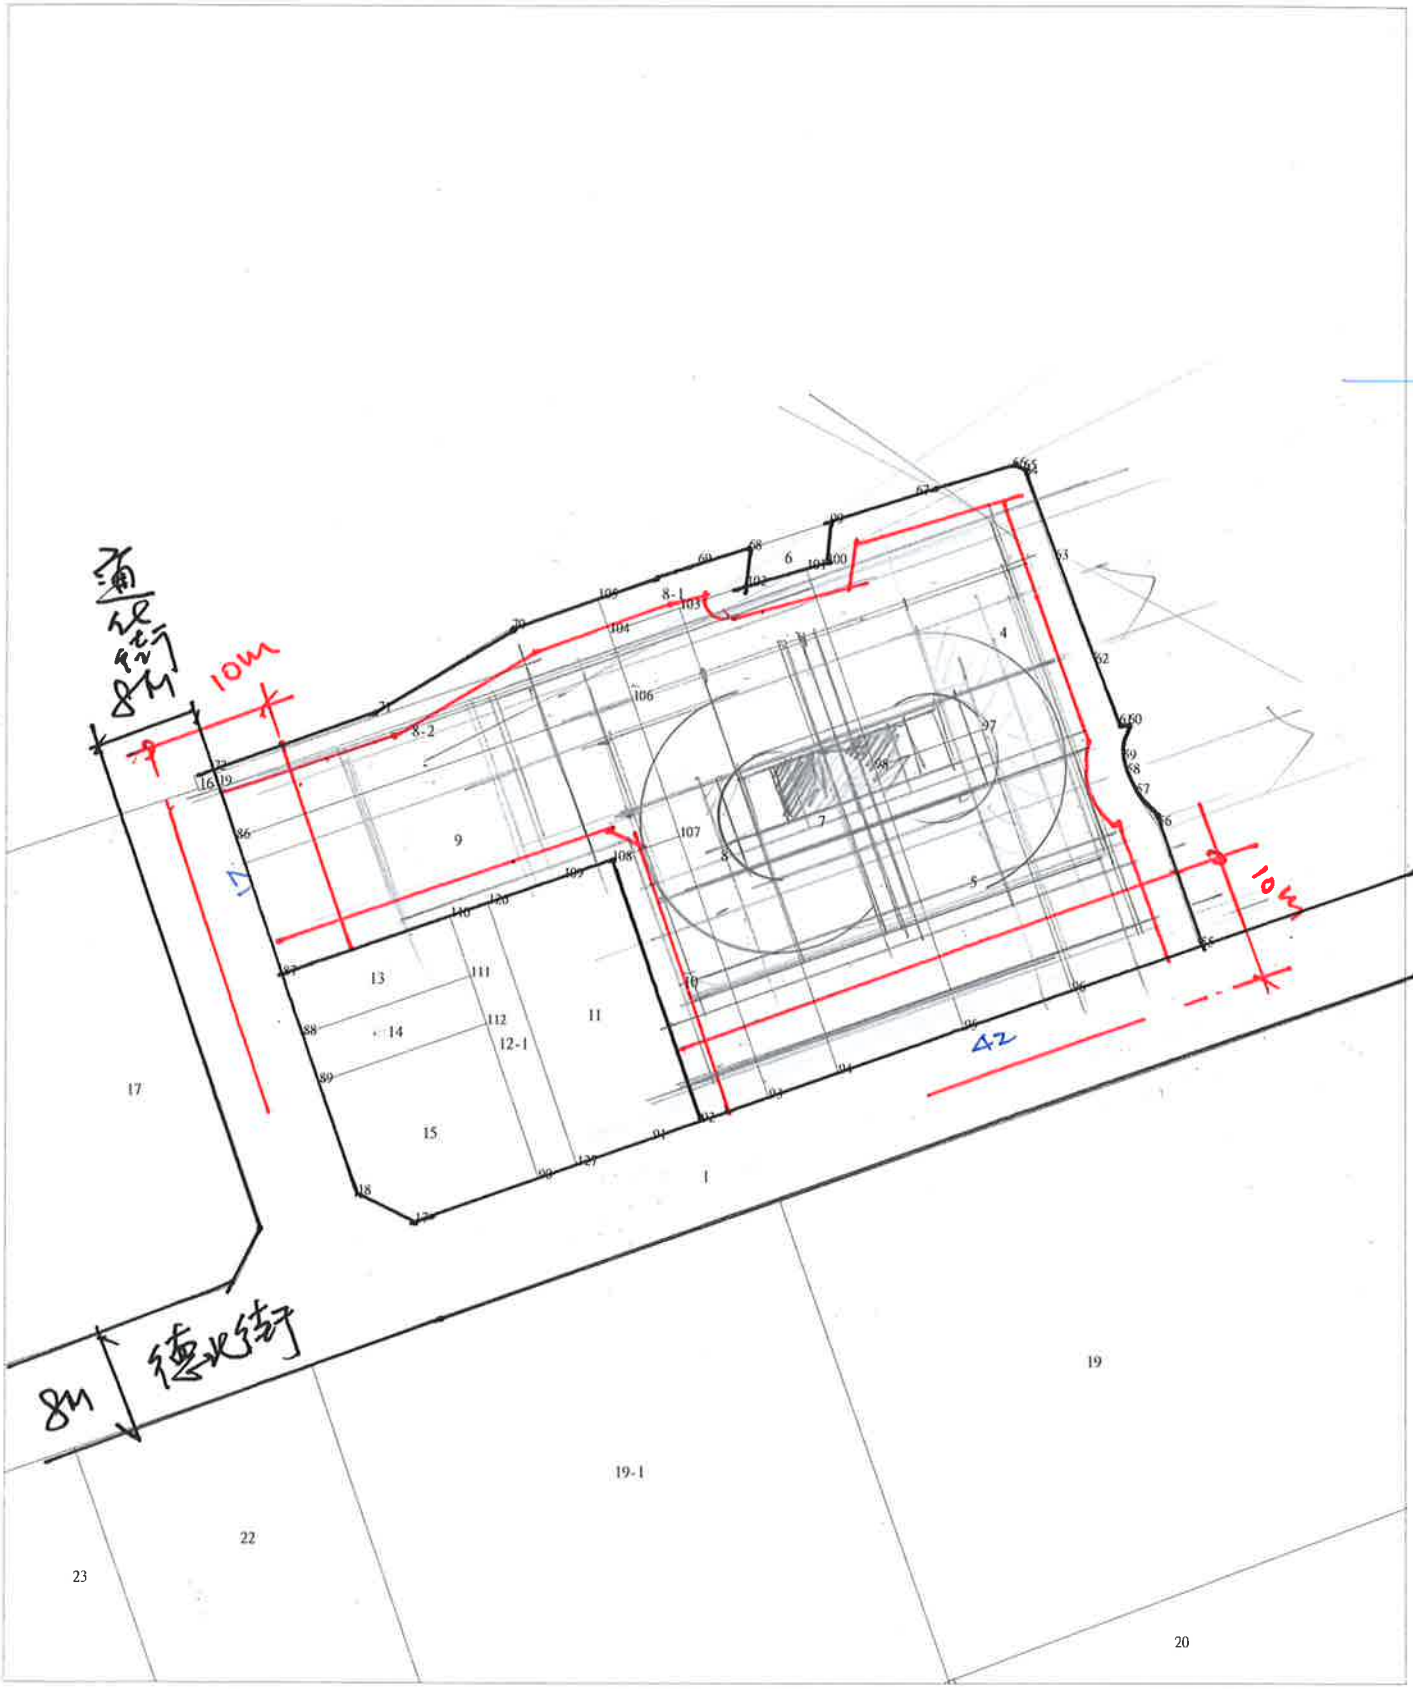

比例尺：1/600　　原比例尺：1/500

本謄本係網路申領之電子謄本，由張文懋自行列印
謄本種類碼：VJG9C8U3VX，可至：https://ep.land.nat.gov.tw 查驗本謄本之正確性
惟為考量檔案傳輸中心之資料負荷度，線上有效查驗期限為三個月。